SELECTED WORK

AHMED ASHRAF

URBAN PLANNING & URBAN DESIGN

Planning strategy, spatial analysis and public-realm design.

AHMED ASHRAF ABDELMAKSOUD

PORTFOLIO

OCTOBER 2026

PROFESSIONAL PROFILE

A PLANNER ACROSS SCALES

Urban planner and urban designer with 9 years of experience in detailed planning, village development, urban design and GIS. Work spans urban surveying, geodatabases, planning solutions, technical review and visual presentation, including coordination with client authorities.

09
YEARS OF EXPERIENCE

04
SURVEY TEAMS LED

08
TEAM MEMBERS

AREAS OF PRACTICE

PLANNING & DELIVERY

Strategic and detailed plans, urban boundaries, village development.

GIS & SPATIAL ANALYSIS

Geodatabases, spatial mapping and cross-referencing of aerial imagery.

PUBLIC REALM & DOCUMENTATION

Streetscapes, hardscape drawings, staking and visual communication.

COMPETITION RECOGNITION

First Place / Cul-de-Sac Urban Design Competition
Madinah, 2026
Design and visual presentation as part of the winning team.

CAREER PROGRESSION

2023-PRESENT	**AFM Engineering Consultants** Urban Planner & GIS Specialist
2022-2023	**Asses Al Benaa** Urban Planner
2021-2022	**Center of Planning & Architectural Studies** Deputy Head of Urban Planning Department
2019-2021	**Julfar Engineering Services** Urban Planner
2017-2019	**Point Engineering Consultations** Urban Planner

EDUCATION

Cairo University / Bachelor's degree in Urban & Regional Planning, 2017
Environmental Planning / Postgraduate coursework since 2025

CORE TOOLS

ArcGIS Pro / AutoCAD / Adobe Photoshop
SketchUp / Lumion / Microsoft Office

SELECTED PROJECTS

01	**FINAA / Cul-de-sac regeneration** Urban design / winning team proposal	04-06
02	**85 Villages / Madinah region** Survey leadership / village development	07-09
03	**Detailed plans / cities & neighborhoods** Road networks / urban blocks / GIS	10-13
04	**75 Villages / Jazan region** Existing conditions mapping / planning	14-15
05	**Village strategic plans / Al Behira** Urban survey through official approval	16-17
06	**King Khaled Road / Sarat Abidah** Streetscape design / visual presentation	18
07	**Al Bukayriyah City Center** Hardscape / documentation / team visualization	19-21
08	**Zakher City Center / Qatar** Visual presentation	22-23
09	**Beni Mazar / graduation project** Academic strategic planning	24
10	**Craft & industrial district** Academic detailed planning	25

Click a project row to jump to its first page.

FINAA | FROM DEAD END TO COURTYARD

Al Gharra, Madinah / Neighborhood regeneration

THE COURTYARD EXPERIENCE

ONE NEIGHBORHOOD. MANY COURTYARDS.

Transform underused dead ends into shared places for shade, walking and daily social life.

STREET & PARKING ORGANIZATION

MY CONTRIBUTION

Urban design, visual presentation and competition poster preparation within the project team.

01 / NEIGHBORHOOD MASTER PLAN

02 / SOUTHERN SERVICE EDGE

03 / WESTERN EDGE

DAILY SERVICES

Mosques / education
Commercial uses
Parks & open space

Walking routes connect the residential courtyards to the service center.

FROM EXISTING STREET TO SHARED COURTYARD

Core competition intervention / existing conditions, design response and sections

01 / EXISTING CONDITION

A STREET WITHOUT A PLACE TO STAY.

Informal parking, limited shade and constrained pedestrian space leave few opportunities for play, seating or daily social life.

02 / EXISTING WIDE STREET

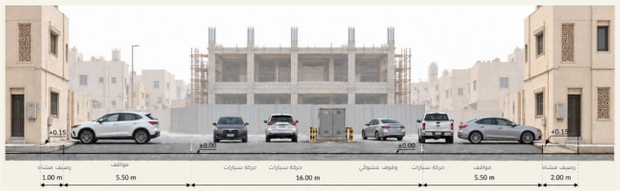

THE DESIGN SHIFT

Organize parking and circulation while introducing a planted, shared public space within the cul-de-sac.

03 / PROPOSED CUL-DE-SAC PLAN

WALK

Connected routes and crossings.

STAY

Seating, play and planted spaces.

ORGANIZE

Defined parking and circulation.

04 / PROPOSED WIDE STREET SECTION

05 / PROPOSED NARROW STREET

A REPEATABLE NEIGHBORHOOD MODEL

The courtyard intervention combines public-space activity, landscape and access within the existing residential street framework.

FINAA | PUBLIC-REALM EXPERIENCE

AI-generated visualizations / illustrative views of the proposed design

COURTYARD & STREET ORGANIZATION

A PLACE TO MEET

Shared seating and shade at the center of the residential street.

THE PEDESTRIAN EDGE

LANDSCAPE & PUBLIC LIFE

Illustrative views explore the proposed setting and atmosphere of everyday neighborhood activity.

AI-GENERATED VISUALIZATIONS / Illustrative representations of the proposed design.

SELECTED PROFESSIONAL WORK

85

VILLAGES

Comprehensive village development

Madinah Region, Saudi Arabia

4
SURVEY TEAMS

8
TEAM MEMBERS

MY CONTRIBUTION

- Urban survey team leadership
- Baseline geodatabase preparation
- Urban boundary delineation
- Indicative planning

AFM Engineering Consultants
Project scope: 85 villages across Badr, Al-Eis, Al-Henakiyah, Khaybar and Wadi Al-Fara.

FROM URBAN SURVEY TO

Indicative planning

Al Murabba / Selected village example

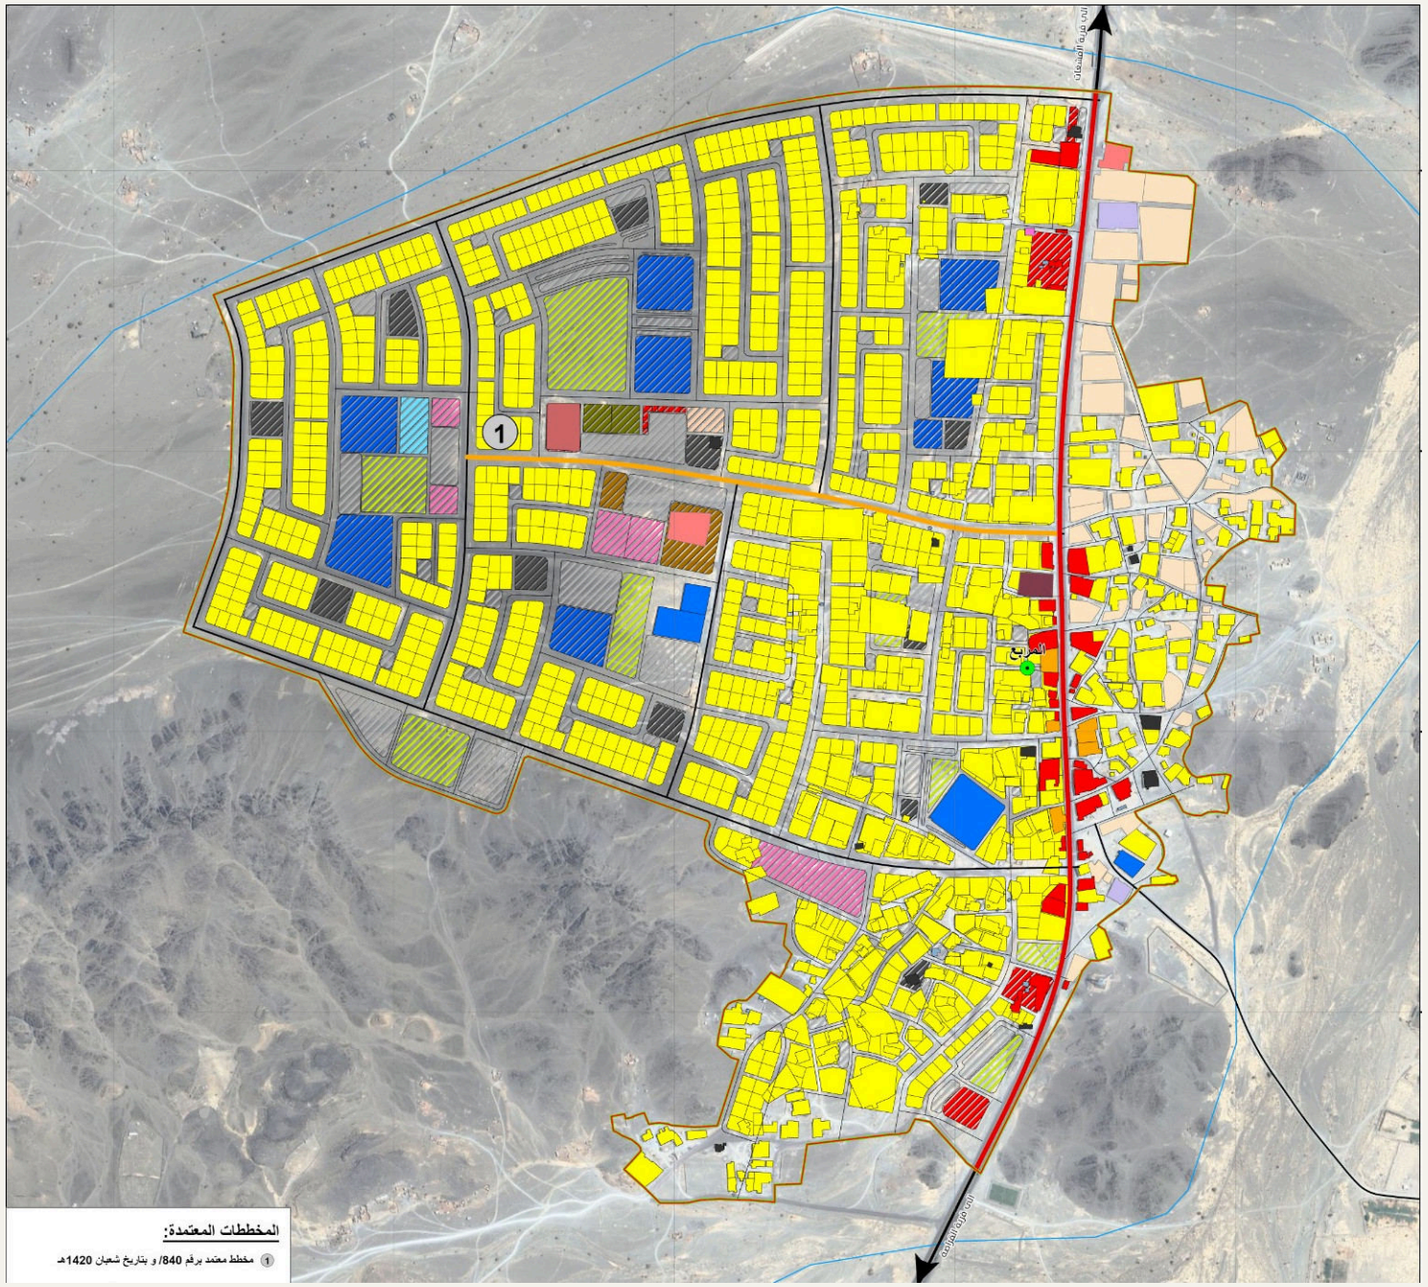

Existing fabric, an approved subdivision and service allocations brought together in one indicative plan.

85 VILLAGES | AL SHAWAMIN

Survey context, existing land use and indicative planning / Wadi Al-Fara

01 Survey context

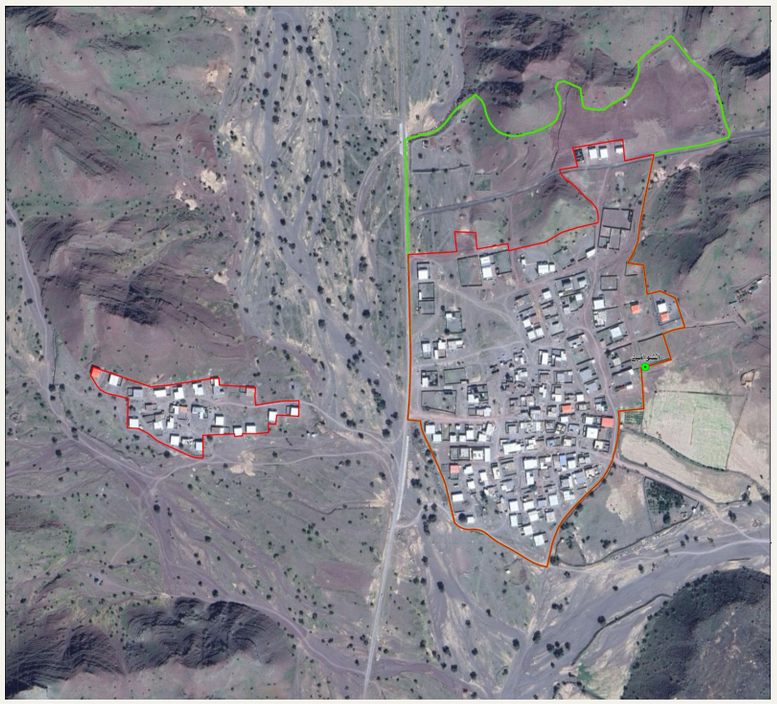

Aerial imagery and settlement boundaries.

02 Existing land use

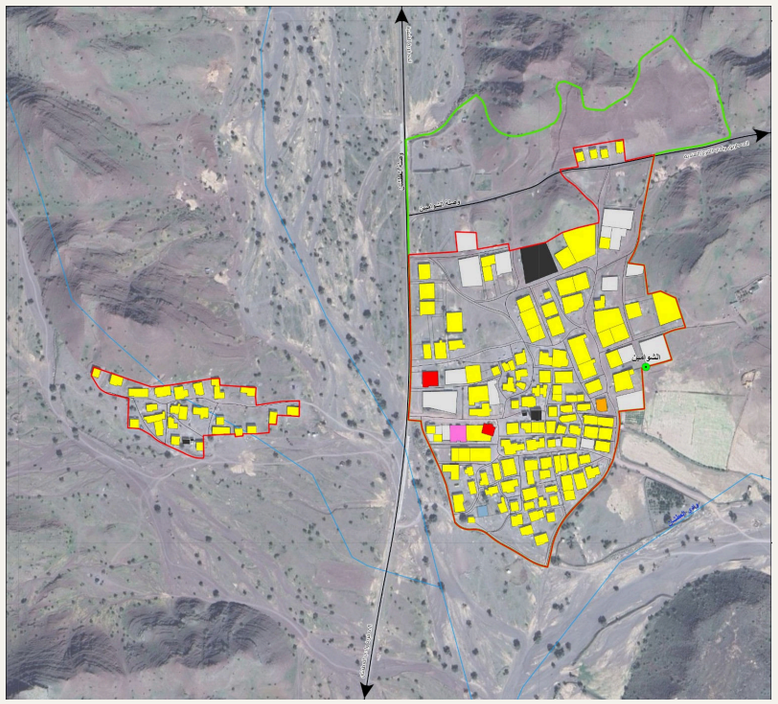

Mapped uses within the existing urban fabric.

03 Indicative plan

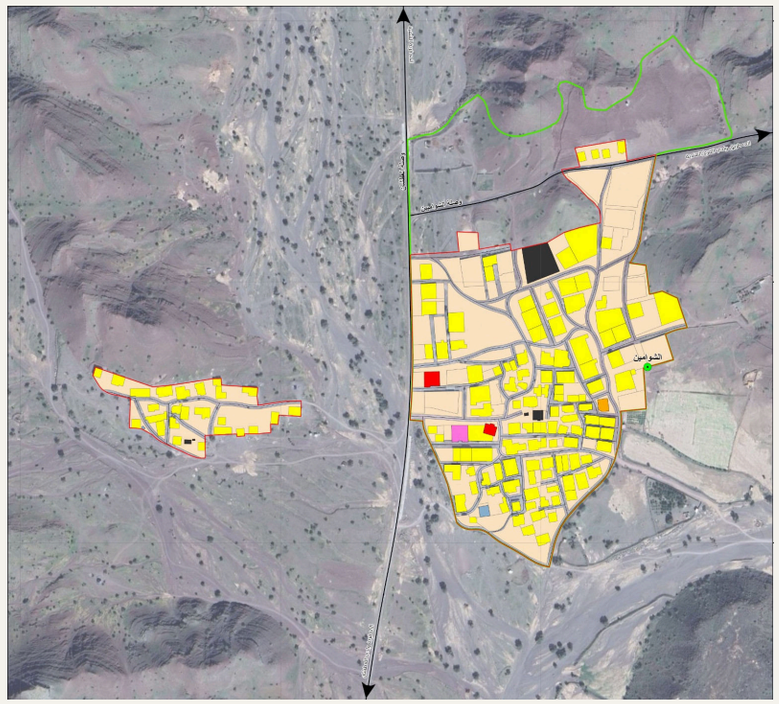

Development areas, uses and road structure.

MY ROLE ACROSS THE WORKFLOW

LEAD

Coordinate four urban survey teams comprising eight members.

PREPARE

Build baseline geodatabases to support planning work.

DELINEATE

Contribute to the definition of urban boundaries.

PLAN

Contribute to the preparation of indicative plans.

85 VILLAGES | AL THAMAD

Indicative plan and development controls / Khaybar

AL THAMAD / KHAYBAR

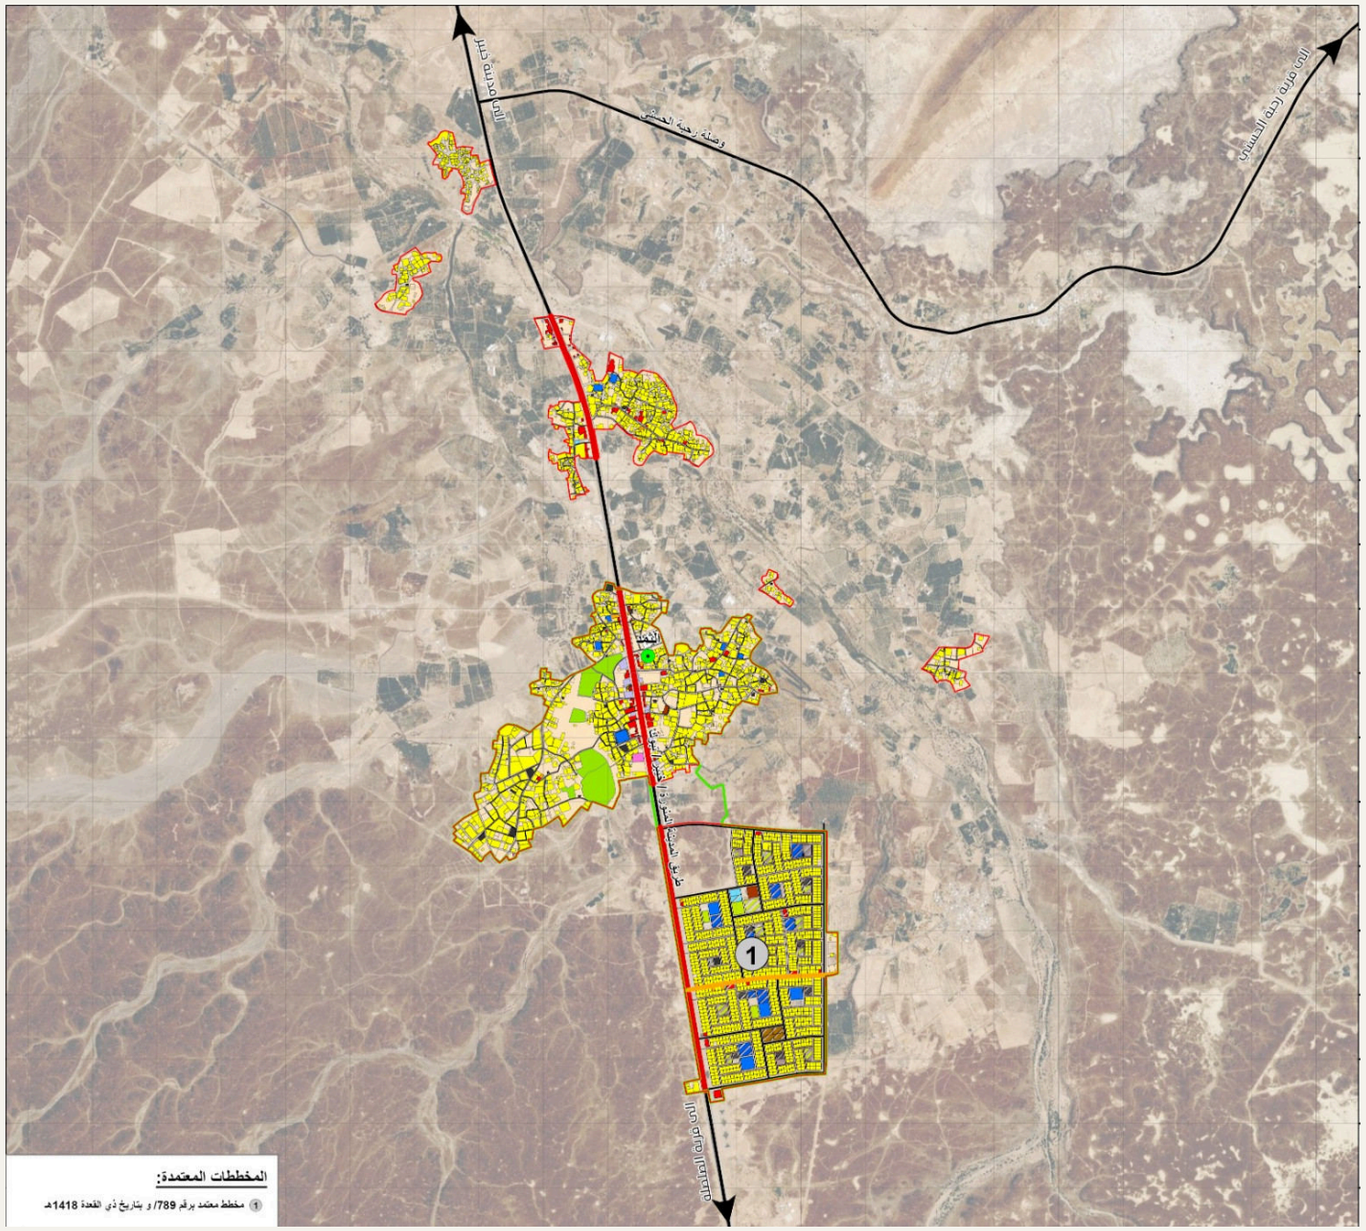

Indicative plan across multiple settlement clusters.
Original planning colors and geometry retained.

RESIDENTIAL CONTROLS

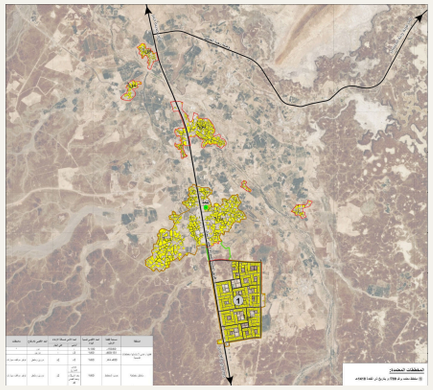

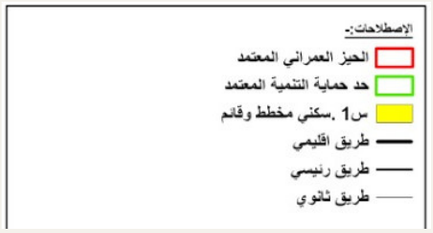

Al Thamad / Residential zoning sheet and source legend.

CORRIDOR CONTROLS

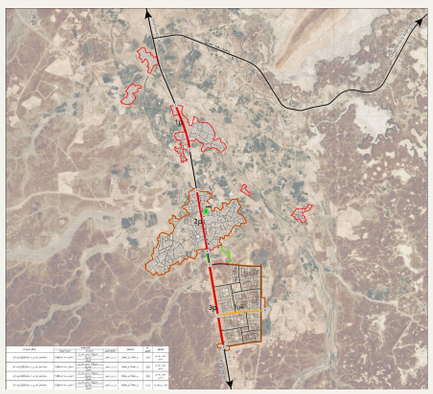

Al Thamad / Corridor controls and source legend.

Selected excerpts from project drawings. Displayed scales vary; consult source sheets for full legends and control schedules.

DUMAT AL JANDAL

Street network development, urban blocks and GIS cartography

01 CITY-SCALE PLAN

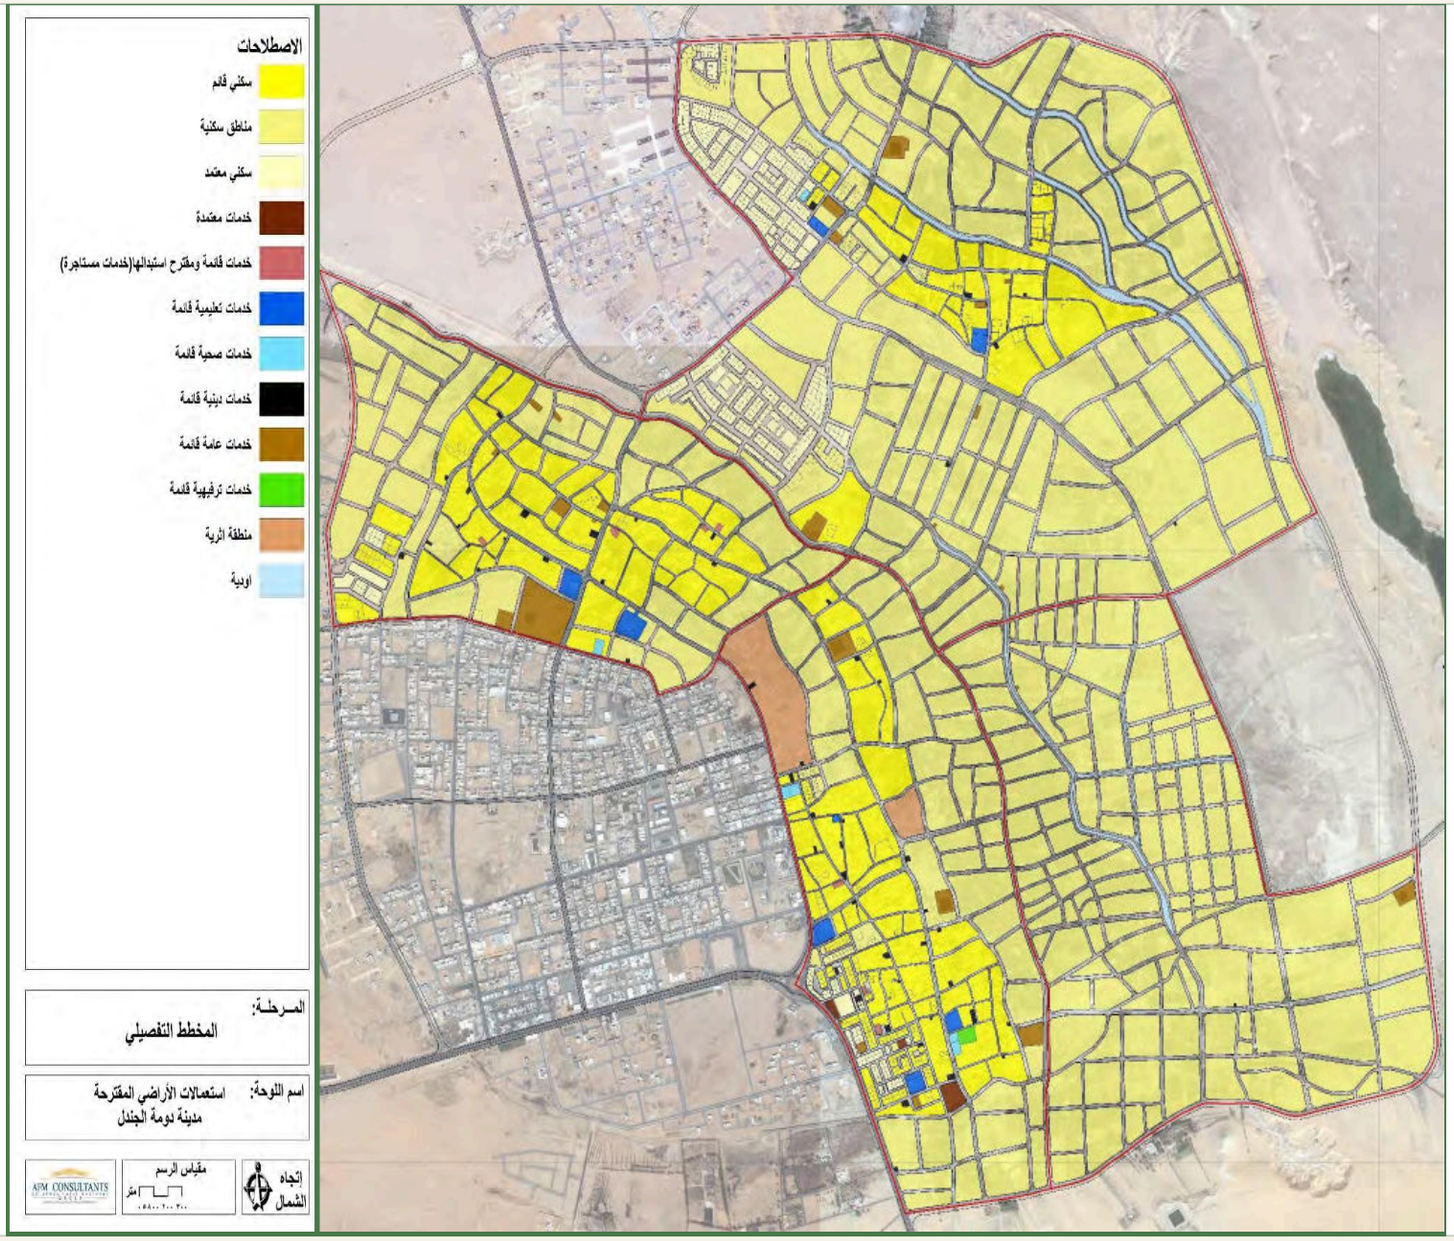

02 SELECTED DISTRICT PLANS

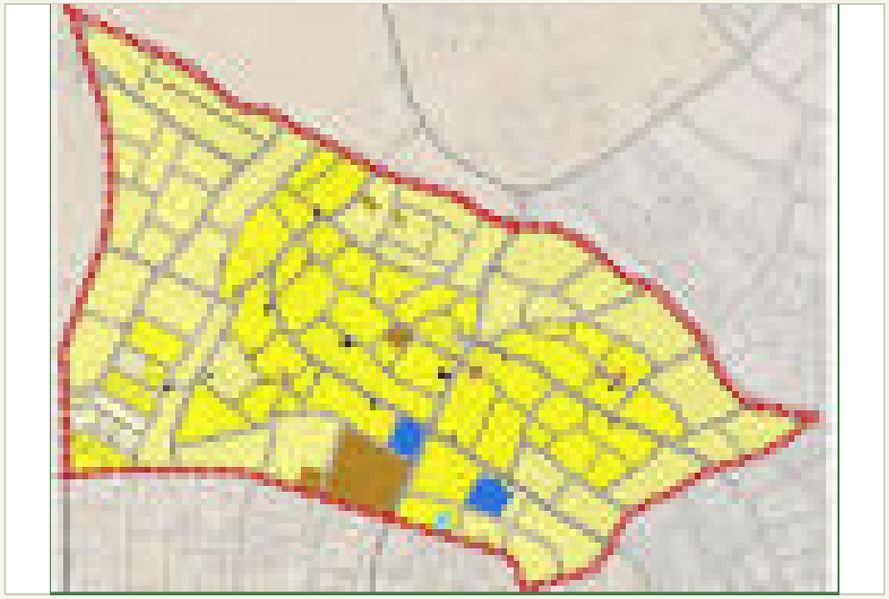

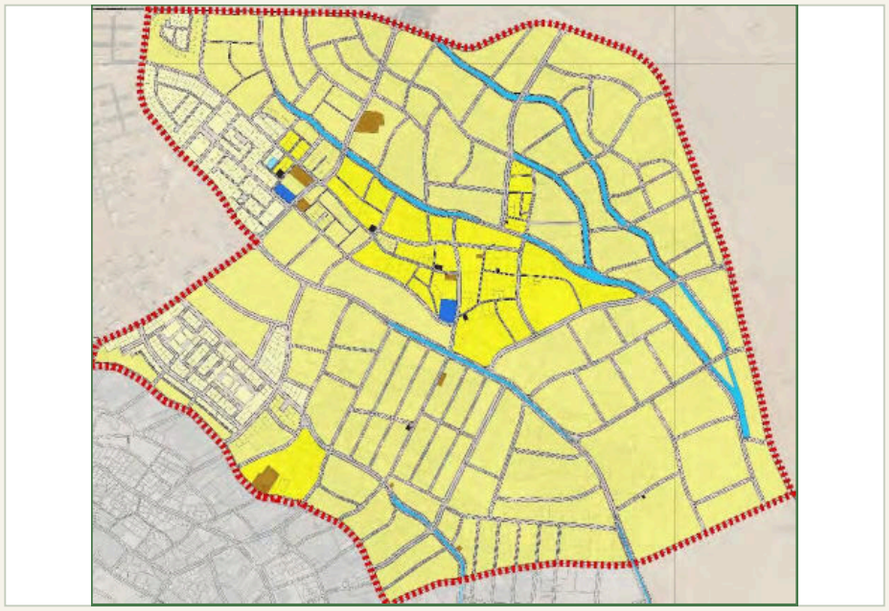

MY CONTRIBUTION

Developed planning solutions to upgrade and widen the existing road network; prepared the proposed street network, street regulation lines, urban blocks and sidewalks, and produced detailed drawings and GIS-based map outputs.

PLANNING WORKFLOW

Existing network > road upgrades > regulation lines
Urban blocks & sidewalks > GIS map outputs

AL QURAYYAT

Street network development, urban blocks and GIS cartography

01 CITY-SCALE PLAN

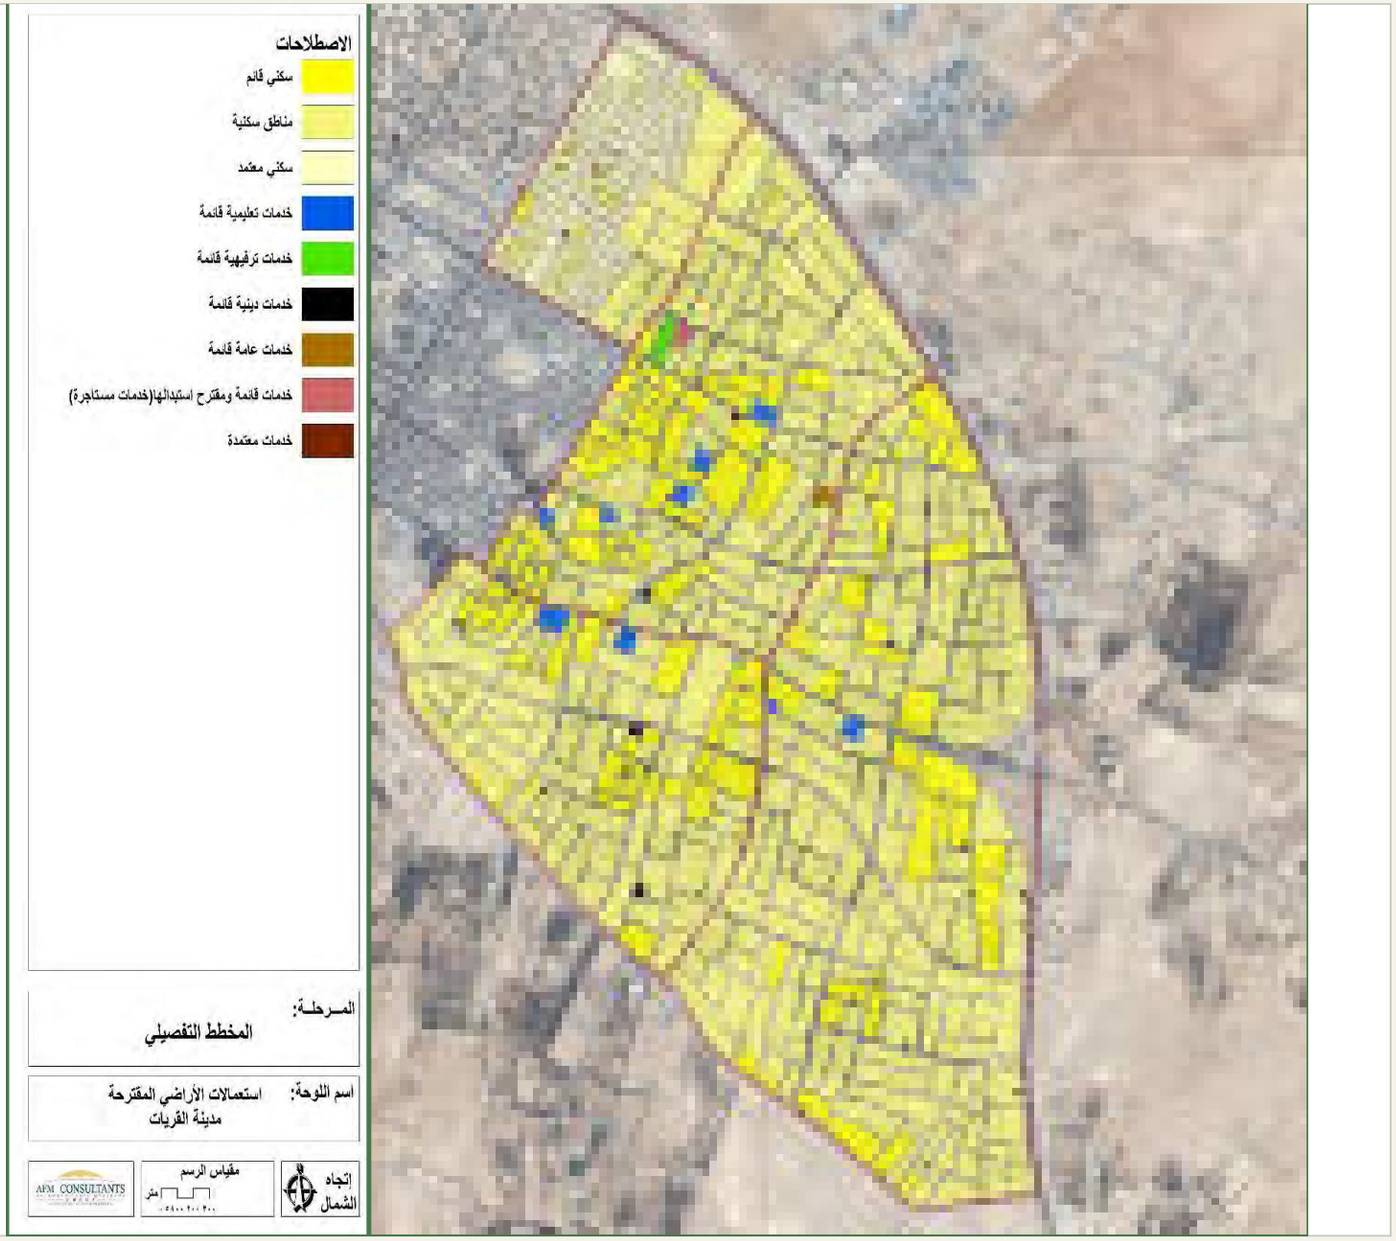

02 SELECTED DISTRICT PLANS

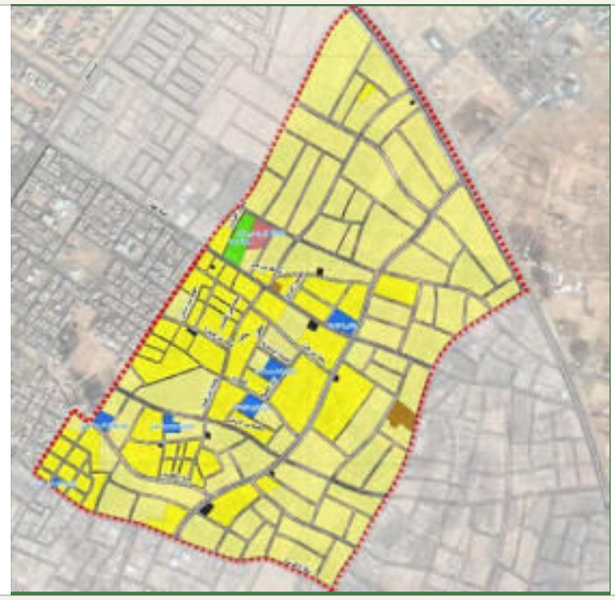

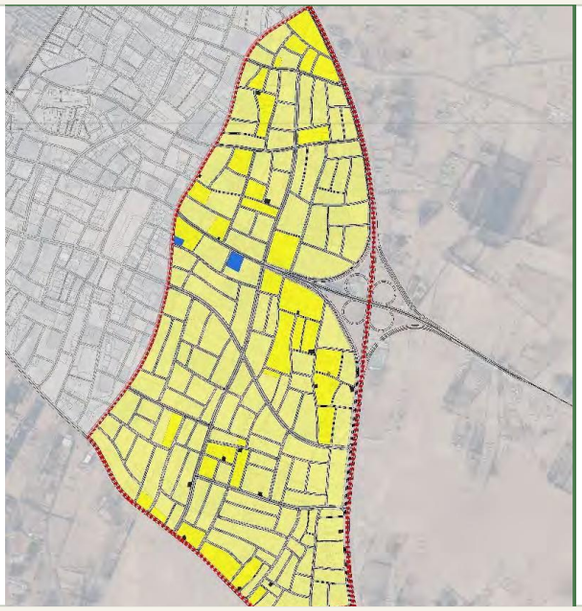

MY CONTRIBUTION

Developed planning solutions to upgrade and widen the existing road network; prepared the proposed street network, street regulation lines, urban blocks and sidewalks, and produced detailed drawings and GIS-based map outputs.

PLANNING WORKFLOW

Existing network > road upgrades > regulation lines
Urban blocks & sidewalks > GIS map outputs

CITY CENTER NEIGHBORHOODS

Street network development, urban blocks and GIS cartography

01 OVERALL NEIGHBORHOOD PLAN

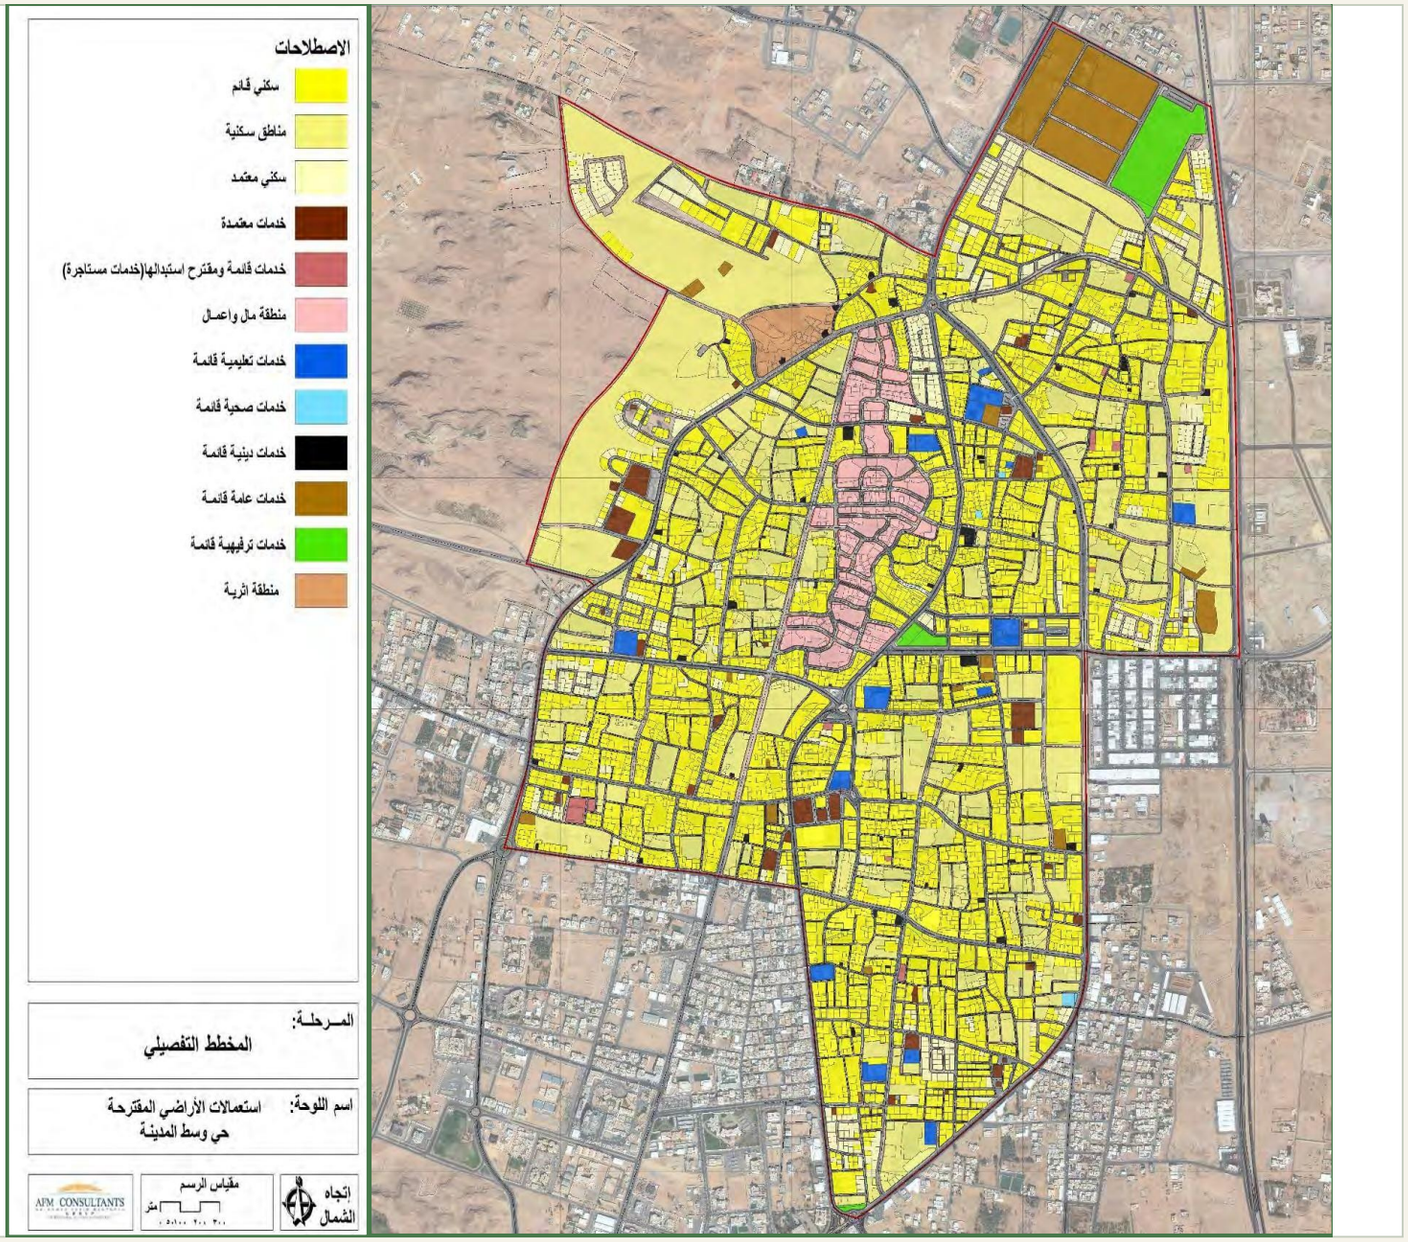

02 SELECTED DISTRICT PLANS

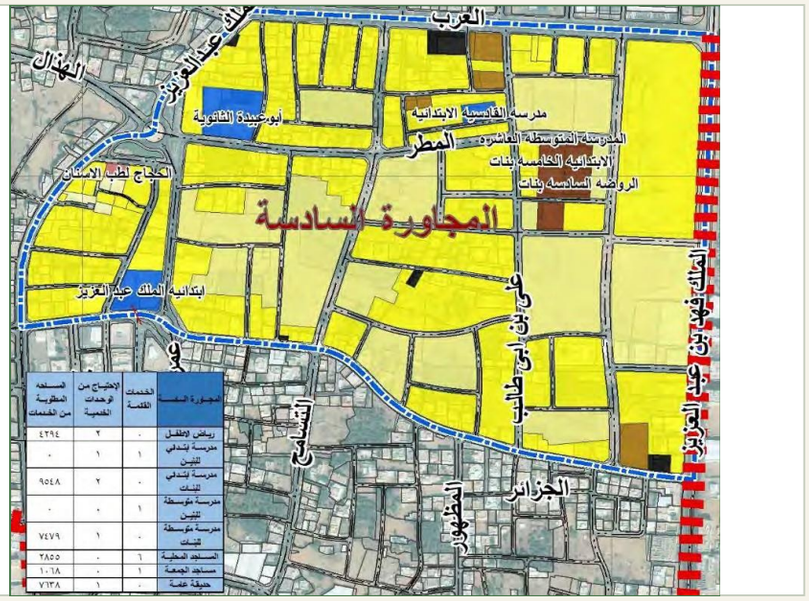

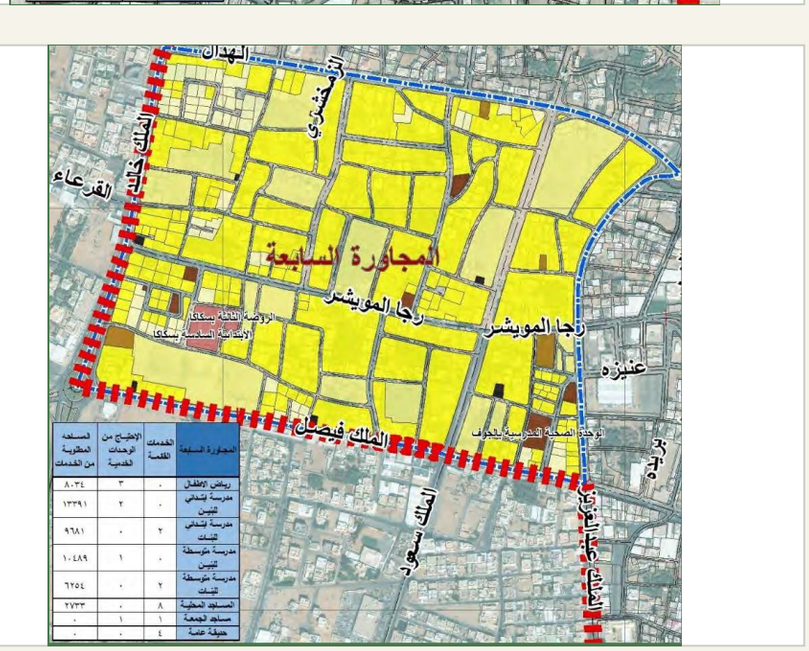

MY CONTRIBUTION

Developed planning solutions to upgrade and widen the existing road network; prepared the proposed street network, street regulation lines, urban blocks and sidewalks, and produced detailed drawings and GIS-based map outputs.

PLANNING WORKFLOW

Existing network > road upgrades > regulation lines
Urban blocks & sidewalks > GIS map outputs

AL LAQAYT NEIGHBORHOOD

Street network development, urban blocks and GIS cartography

01 OVERALL NEIGHBORHOOD PLAN

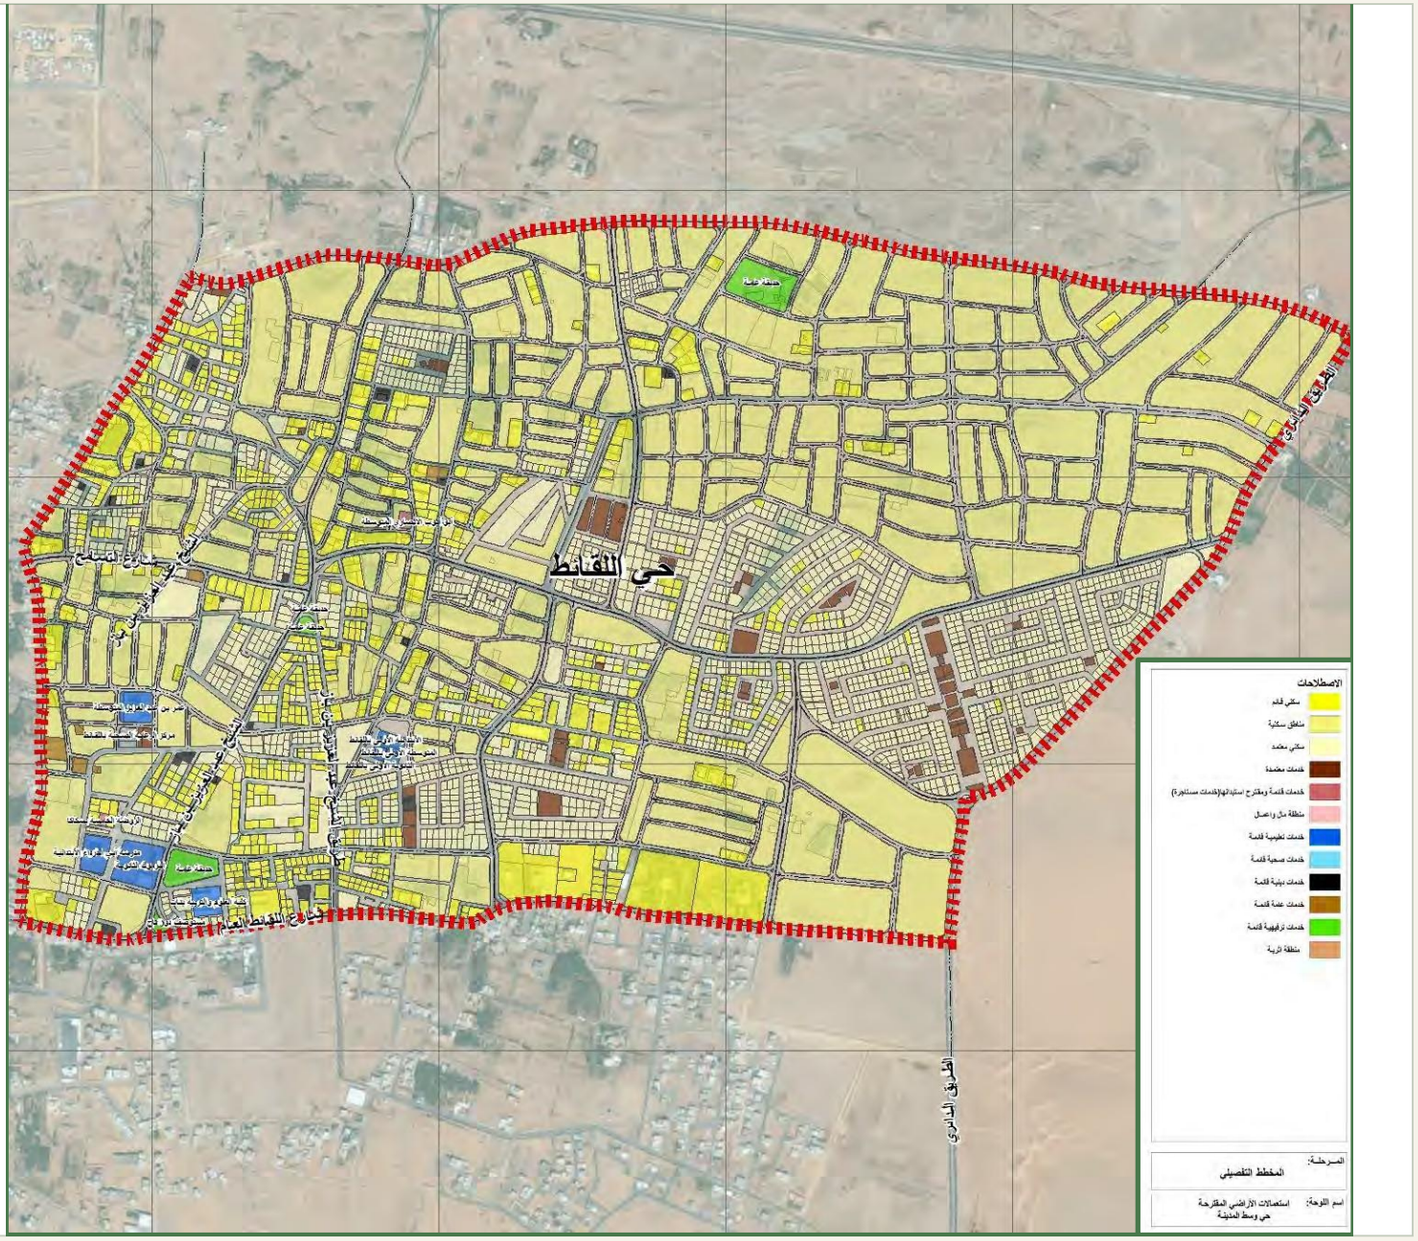

02 SELECTED DISTRICT PLANS

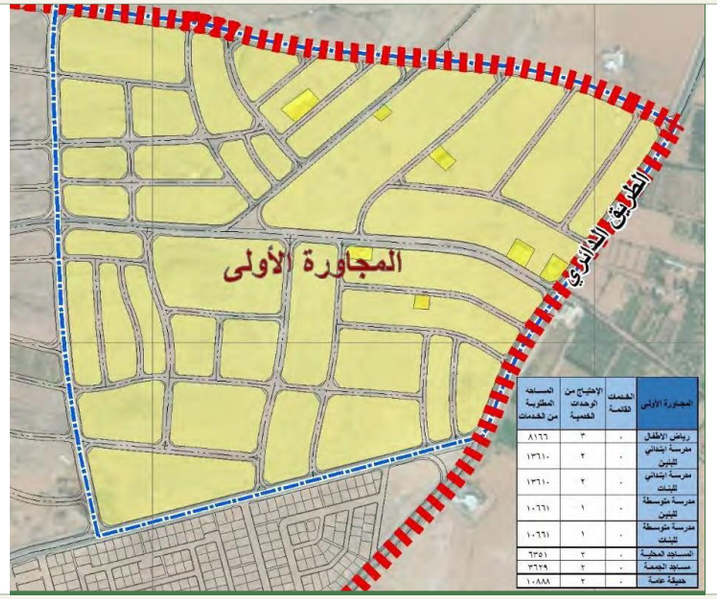

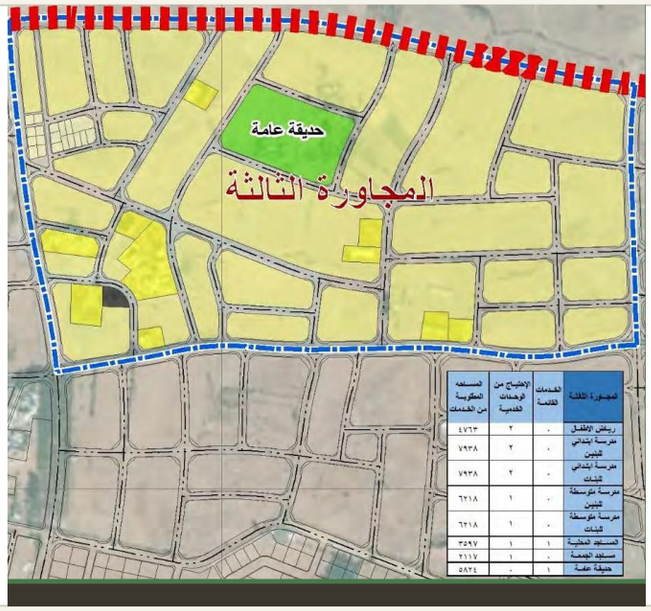

MY CONTRIBUTION

Developed planning solutions to upgrade and widen the existing road network; prepared the proposed street network, street regulation lines, urban blocks and sidewalks, and produced detailed drawings and GIS-based map outputs.

PLANNING WORKFLOW

Existing network > road upgrades > regulation lines
Urban blocks & sidewalks > GIS map outputs

75 VILLAGES | EXISTING CONDITIONS

Selected mapping outputs / urban survey, spatial analysis and planning

01 / LAND-USE MAPPING

02 / SPATIAL CONTEXT & BOUNDARY

MY CONTRIBUTION

Prepared existing-condition drawings and urban analysis, developed planning solutions, and produced plans and presentation outputs within the project team.

03 / SUPPORTING MAPPING OUTPUTS

LAND-USE KEY

- Residential
- Under construction
- Commercial
- Public services

The overall project scope covers 75 villages.

75 VILLAGES | SETTLEMENT STRUCTURE

Selected mapping outputs / development of planning solutions

04 / URBAN EXTENT & SETTLEMENT CONTEXT

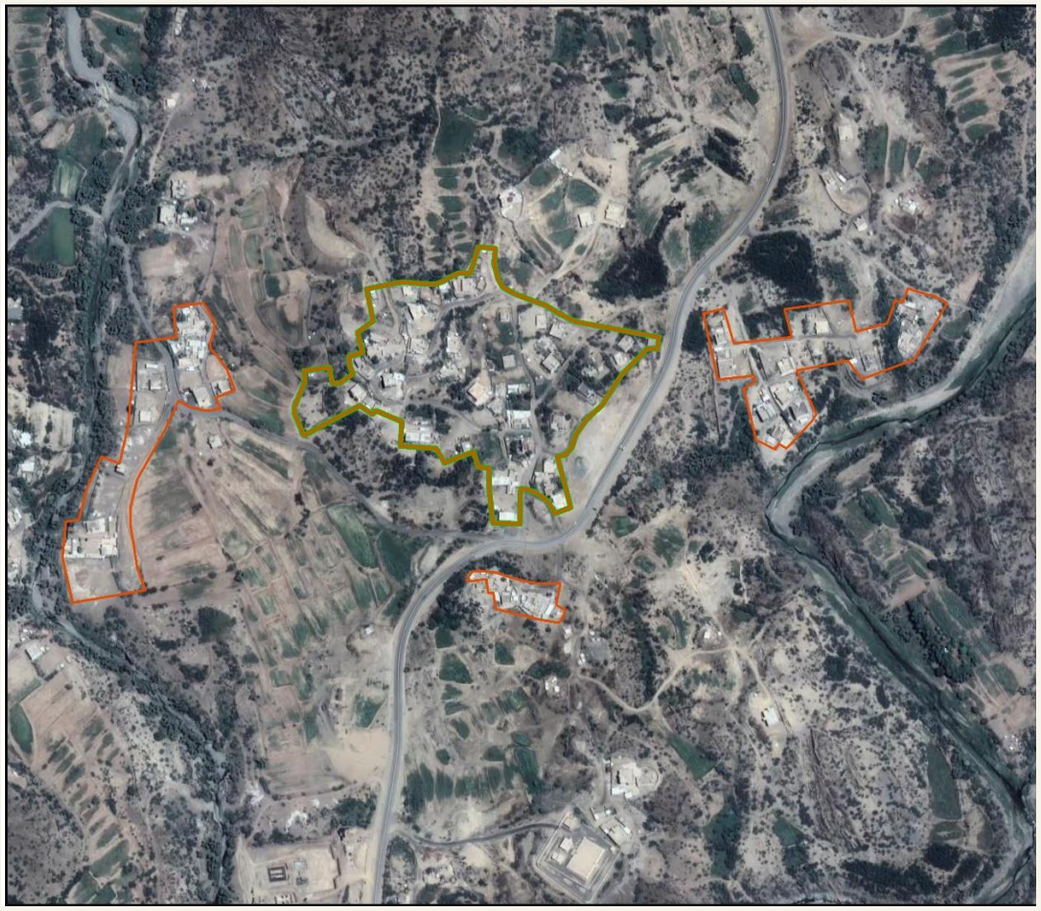

05 / LAND-USE MAPPING

FROM ANALYSIS TO PLANNING SOLUTIONS

Contribution covered existing-condition mapping, urban analysis, planning solutions, plan preparation and visual presentation.

PLANNING WORKFLOW

Existing-condition drawings > urban analysis > planning solutions > plan preparation > final presentation

06 / SUPPORTING MAPPING OUTPUTS

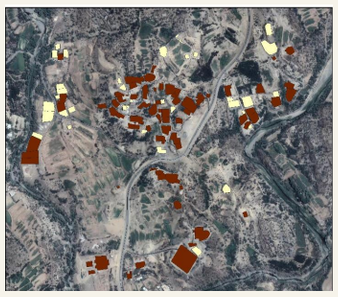

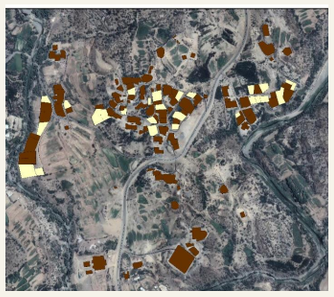

AL BEHIRA | SURVEY & ANALYSIS

Ghonem Shata & Elnazara / selected case: Ghonem Shata

01 / LAND USE & SETTLEMENT PATTERN

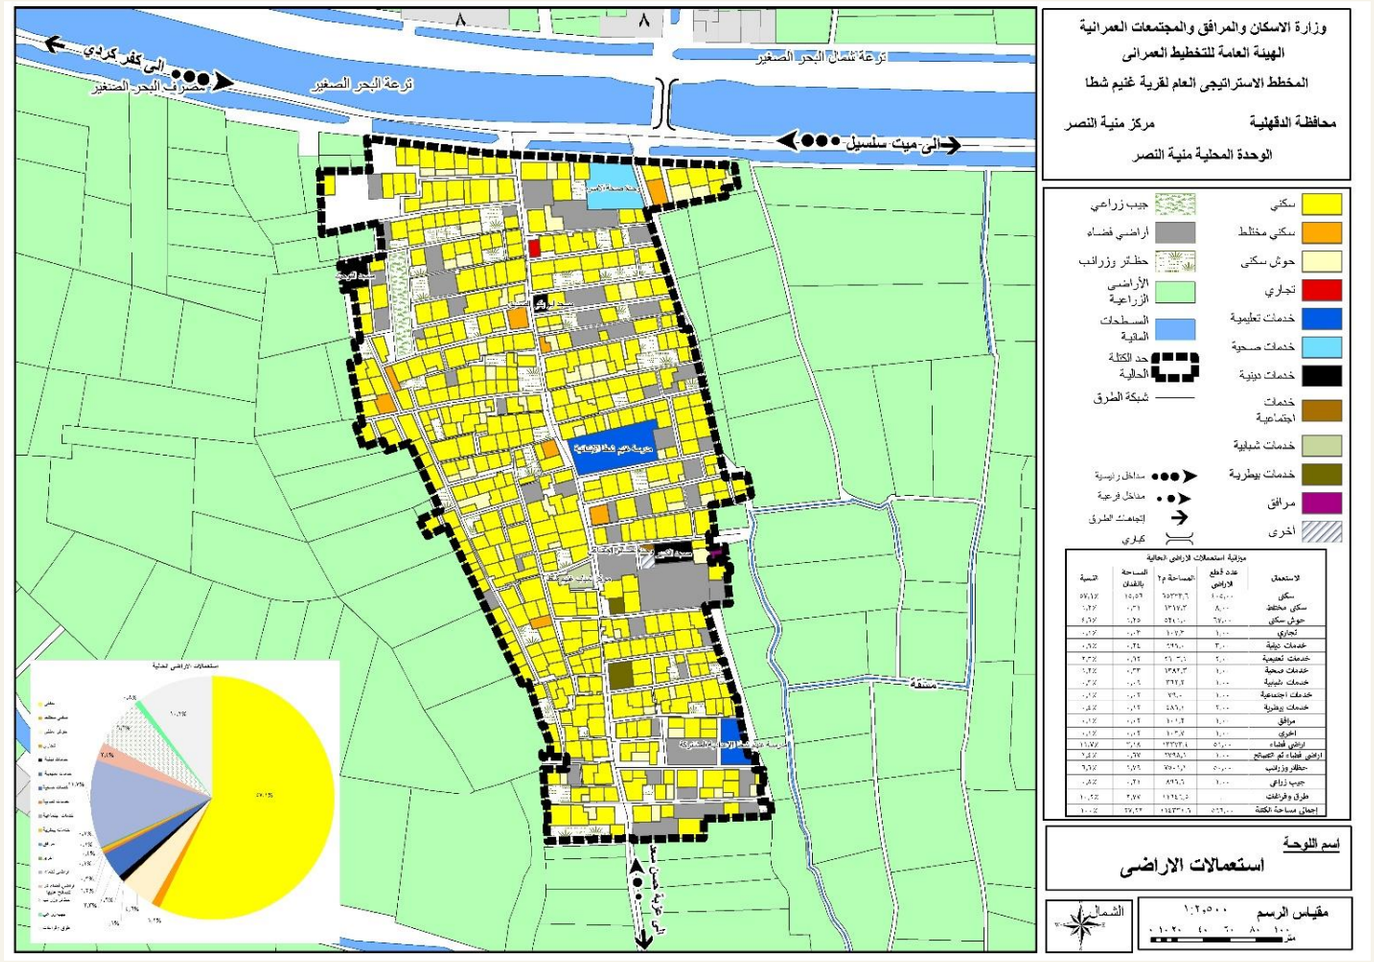

02 / DEVELOPMENT CONSTRAINTS

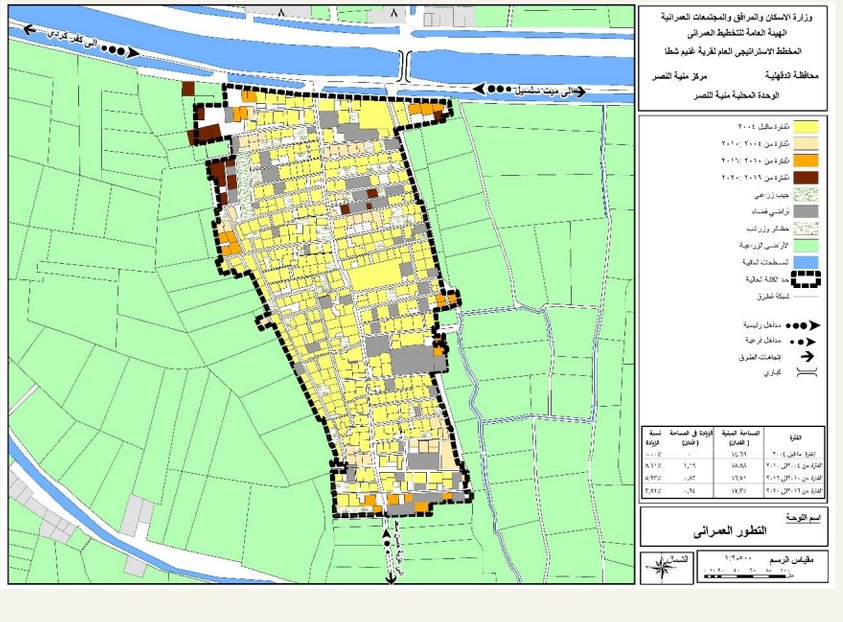

FROM FIELD SURVEY TO ANALYSIS

Participation spanned urban survey, existing-condition mapping and analysis, planning solutions, drawing preparation and final presentation.

03 / BUILDING HEIGHTS

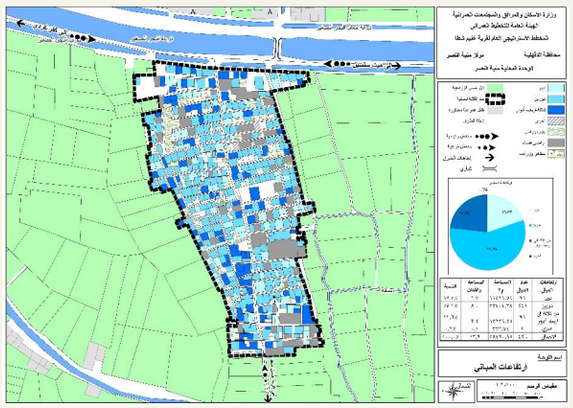

04 / BUILDING CONDITION

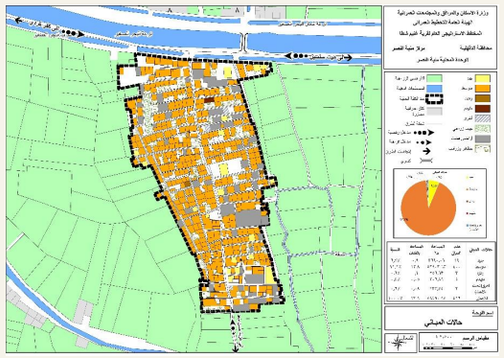

05 / CONSTRUCTION MATERIALS

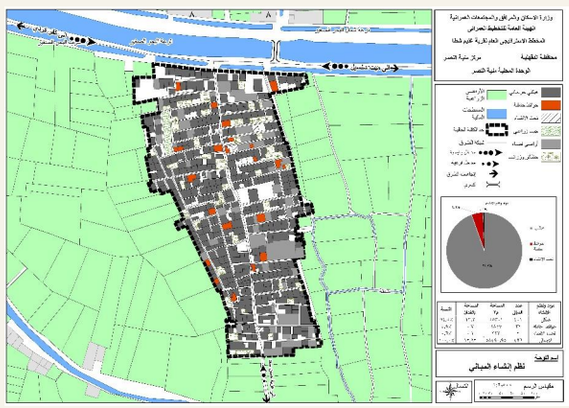

AL BEHIRA | PLANNING & APPROVAL

Urban-boundary documentation and official approval record

06 / URBAN BOUNDARY DOCUMENTATION

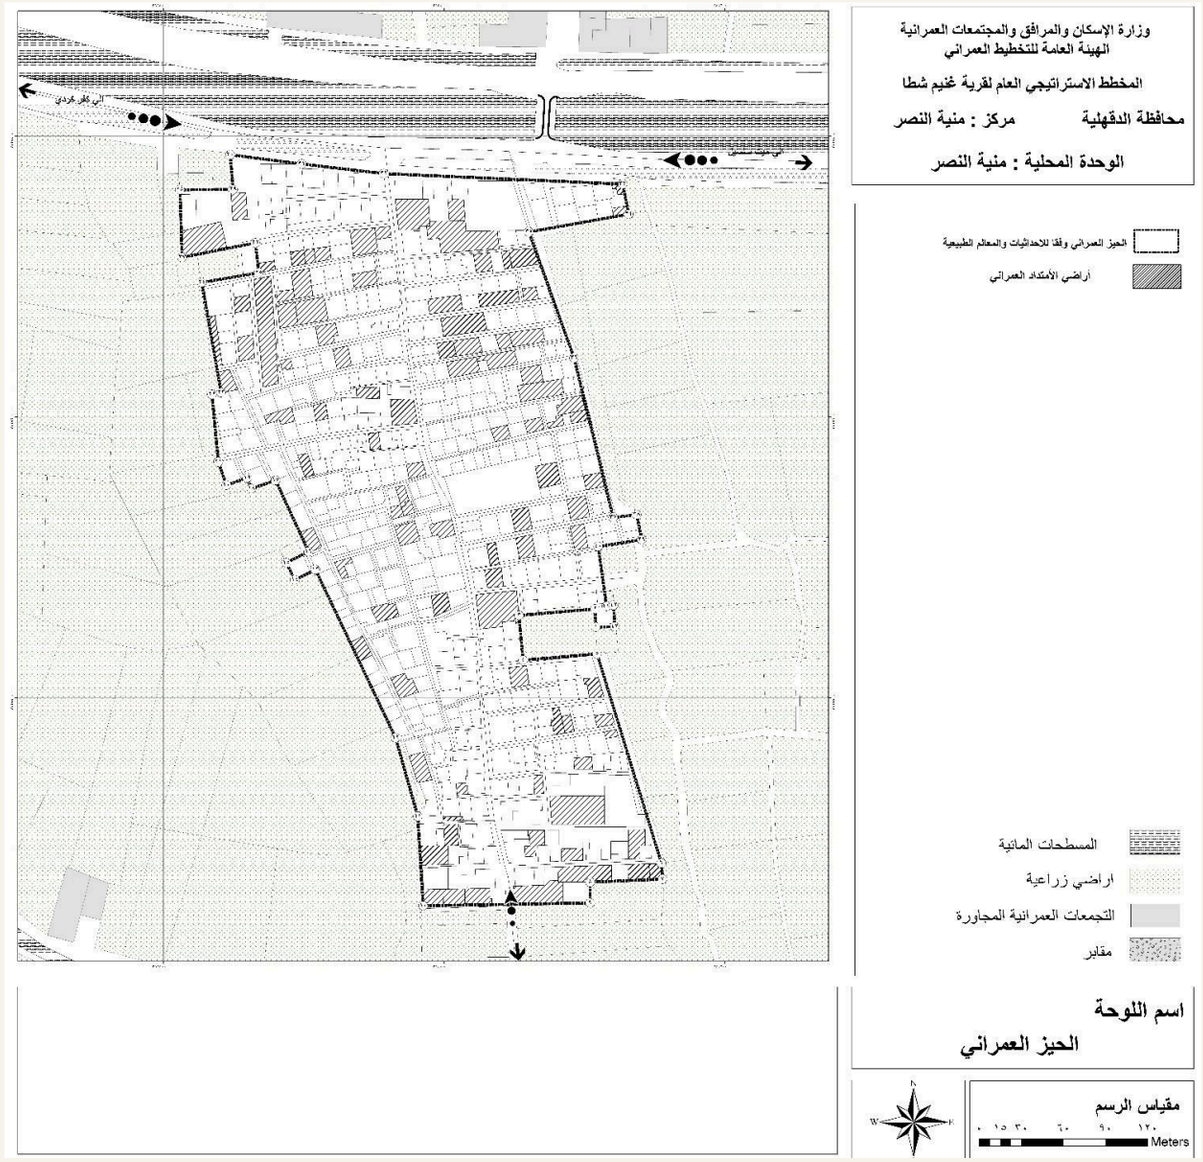

07 / APPROVAL RECORD

الهيئة العامة للتخطيط العمراني
اللجنة الدائمة لاعتماد الاحوزة العمرانية لمدن وقرى الجمهورية
المشكلة بالقرارين الوزاريين رقمى (١٦٩_٥٠٢) لسنة ٢٠١٦

قرار اعتماد الحيز العمراني

قرية: غنيم شطا — الوحدة المحلية: منية النصر

مركز: منية النصر — محافظة: الدقهلية

في ضوء قانون البناء الصادر بالقانون رقم ١١٩ لسنة ٢٠٠٨ تقوم الهيئة العامة للتخطيط العمراني باعداد الاحوزة العمرانية للمدن والقرى التابعة للمحافظات

تم عرض المشروع على اللجنة الدائمة المشكلة بالقرارين الوزاريين رقمى (١٦٩_٥٠٢) لسنة ٢٠١٦ لاعتماد الاحوزة العمرانية لمدن وقرى الجمهورية .

وبعد الدراسة قررت اللجنة الاتى:-

- اعتماد الحيز العمراني للقرية كما هو موضح بالخريطة وذلك بمسطح إجمالى ٢٦,٢٩ فدان بطاقة إستيعابية ١٣٠٣ بكثافة سكانية ٤٩,٥٠ ش/ف

عدم الالتزام بتطبيق قانون البناء الصادر بالقانون رقم ١١٩ لسنة ٢٠٠٨ ولائحته التنفيذية عند إصدار الترخيص بالبناء وأية إجراءات داخل الحيز العمراني المعتمد للعزبه أو الكفر أو النجع

حظر إقامة أية مبانى أو منشآت خارج الحيز العمراني المعتمد إلا فى الحالات المستثناه المنصوص عليها فى القانون رقم ١١٩ لسنة ٢٠٠٨ قبل الترخيص بالبناء وبعد الرجوع لوزارة الزراعة

يتم تطبيق الاشتراطات البنائية لمعتمدة تقنية إتباع لها (عزبة/كفر/نجع) وفى حالة تبعية (عزبة/كفر/نجع) لمدينة تطبق الاشتراطات البنائية للقرب كونية

أعضاء اللجنة

د.م/ مها محمد فهيم محمود فهيم
د.م/ ياسر عبدالحميد محمود حلمى
د.م / أحمد سعد أبومريح
م / حلمى محمد أحمد عبيد
المستشار / محمد ممدوح سالم
د / اشرف عبد القنى محمد
د/ سعد احمد عبد الحميد عامر
م / نجوي السيد ابراهيم
م / هدى محمود هاشم

م / علية السيد عبد الرازق
م / سمير أحمد محمود الروبى
م / محمود عبد الفتاح رجب
م / ايهاب سمير عبد القادر
ا / يسري مصطفى سلطان
م / علاء عمر عبان
م / الشافعي محمد مئونى
م / ناهد نجيب اسرائيل

المدير العام المختص/
ممثل المحافظة/

رئيس الامانة الفنية للجنة :
م/ شربن كمال

رئيس اللجنة

المهندس/ علاء الدين عبد الفتاح على

08 / BOUNDARY PLAN

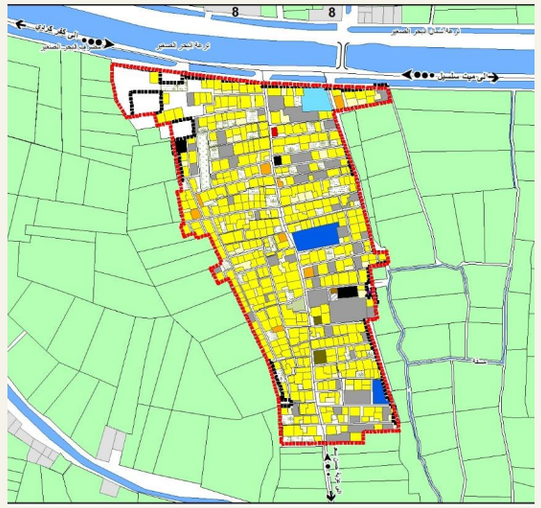

09 / SERVICE LOCATIONS

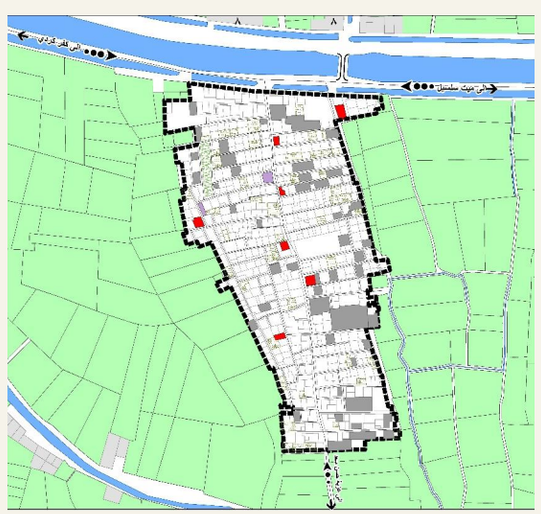

MY CONTRIBUTION

Contributed across project stages, from urban surveying and analysis to planning solutions, drawings and visual presentation, continuing through to official approval.

PROJECT OUTCOME

Official approval of the planning outputs. The selected case includes the urban-boundary plan and its approval record.

KING KHALED ROAD

Sarat Abidah, Saudi Arabia / Urban design & Photoshop presentation

01 STREETSCAPE DESIGN PLAN

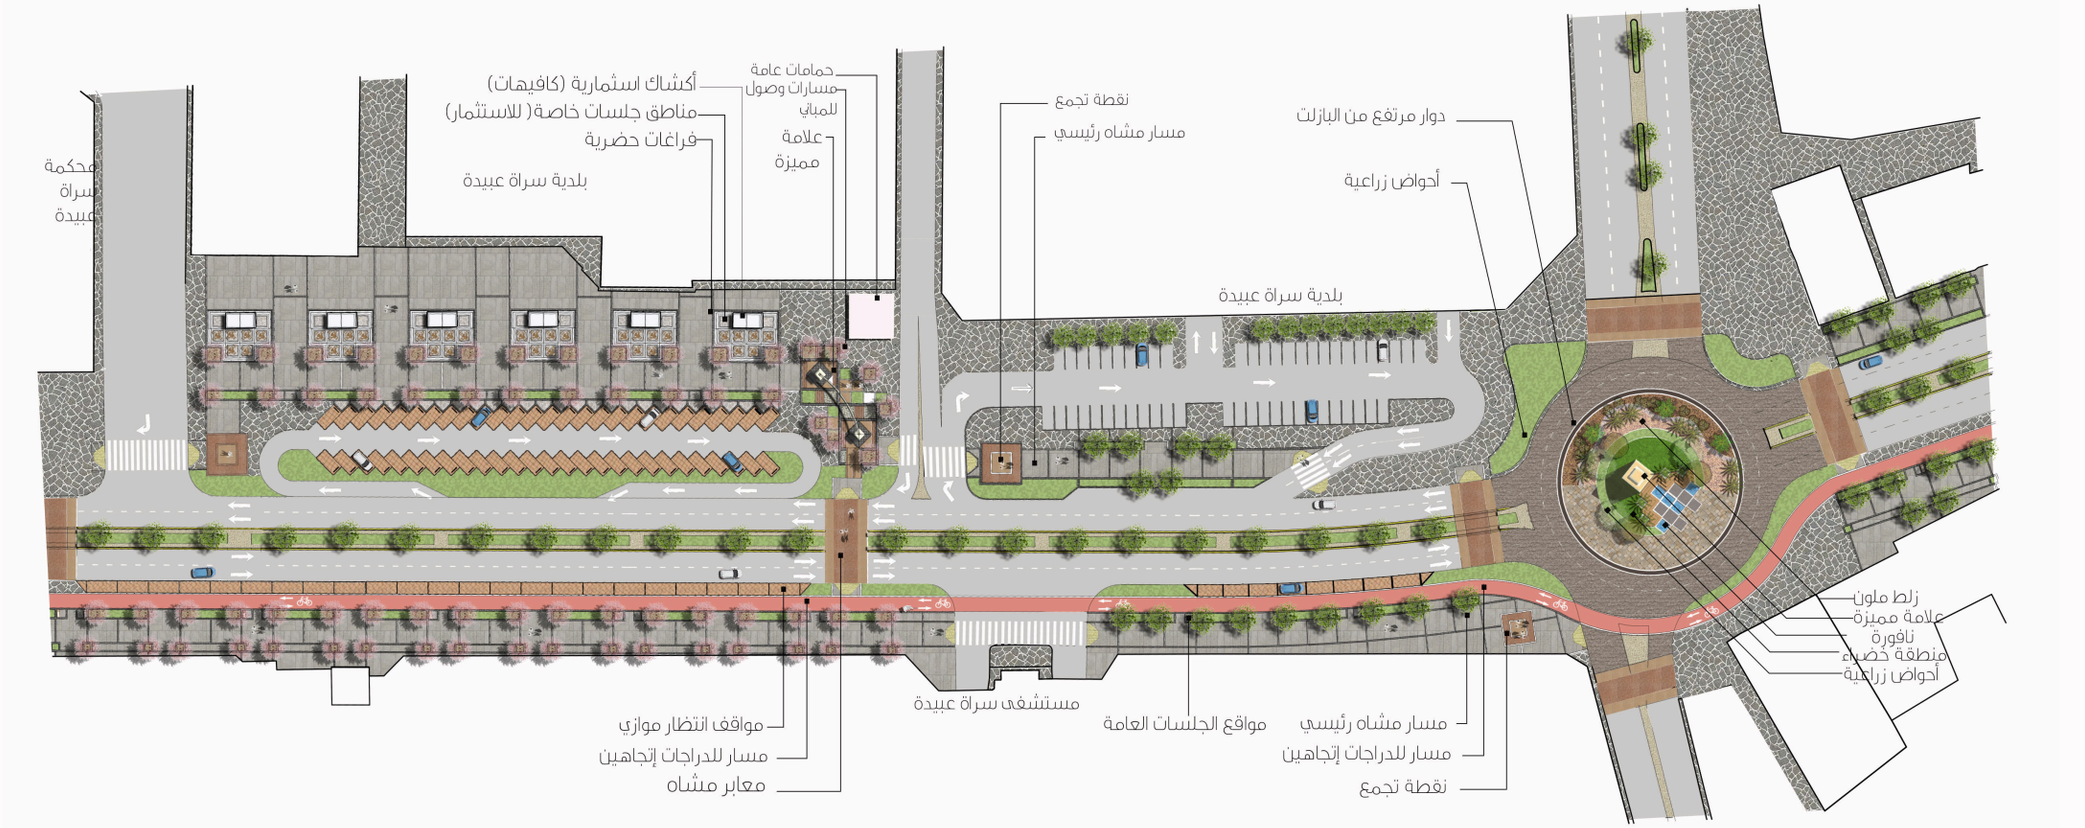

02 OVERALL CORRIDOR

03 ROUNDABOUT DETAIL

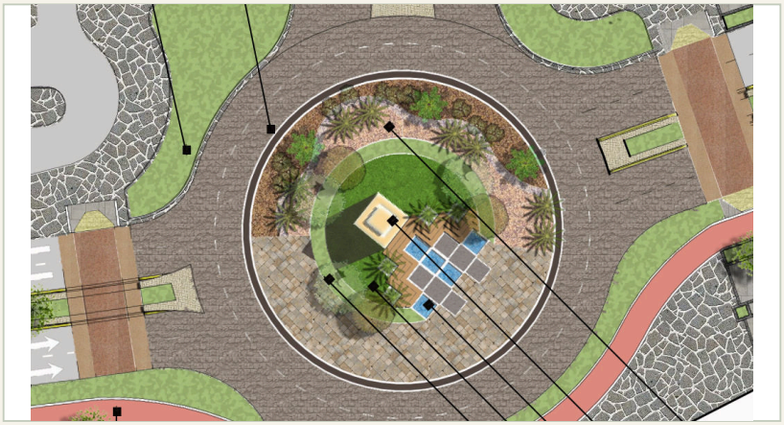

04 STREETSCAPE DETAIL

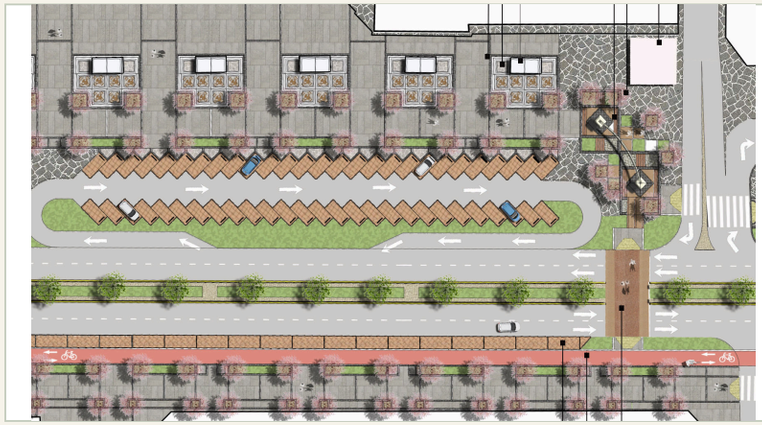

MY CONTRIBUTION

Developed the urban design and prepared plan visualizations using Photoshop.

DESIGN ELEMENTS SHOWN

Pedestrian crossings, parking, a cycle route, seating areas and landscaping.

AL BUKAYRIYAH | HARDSCAPE LAYOUTS

Technical development, layout drawings and construction documentation

MY CONTRIBUTION

Development and production of hardscape drawings from the design stage through construction documentation.

DRAWING PACKAGE

Hardscape layouts
Detail drawings
Staking plans

PROJECT CONTEXT

Point Engineering Consultations
Project location: Saudi Arabia
Professional work: 2017-2019

Primary role: technical drawing production.
Additional contribution: participation in 3D visualization.

PUBLIC-SPACE LAYOUTS

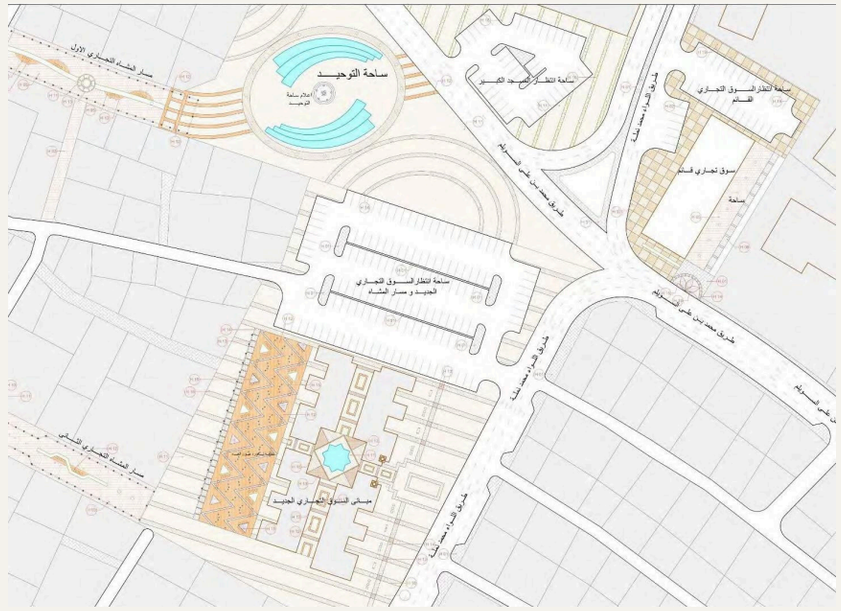

Selected hardscape layouts showing paving composition and the arrangement of public-space elements.

LINEAR HARDSCAPE TREATMENT

AL BUKAYRIYAH | DETAILS & SETTING-OUT

Dimensioned hardscape details and staking plans

PAVING & FEATURE DETAILS

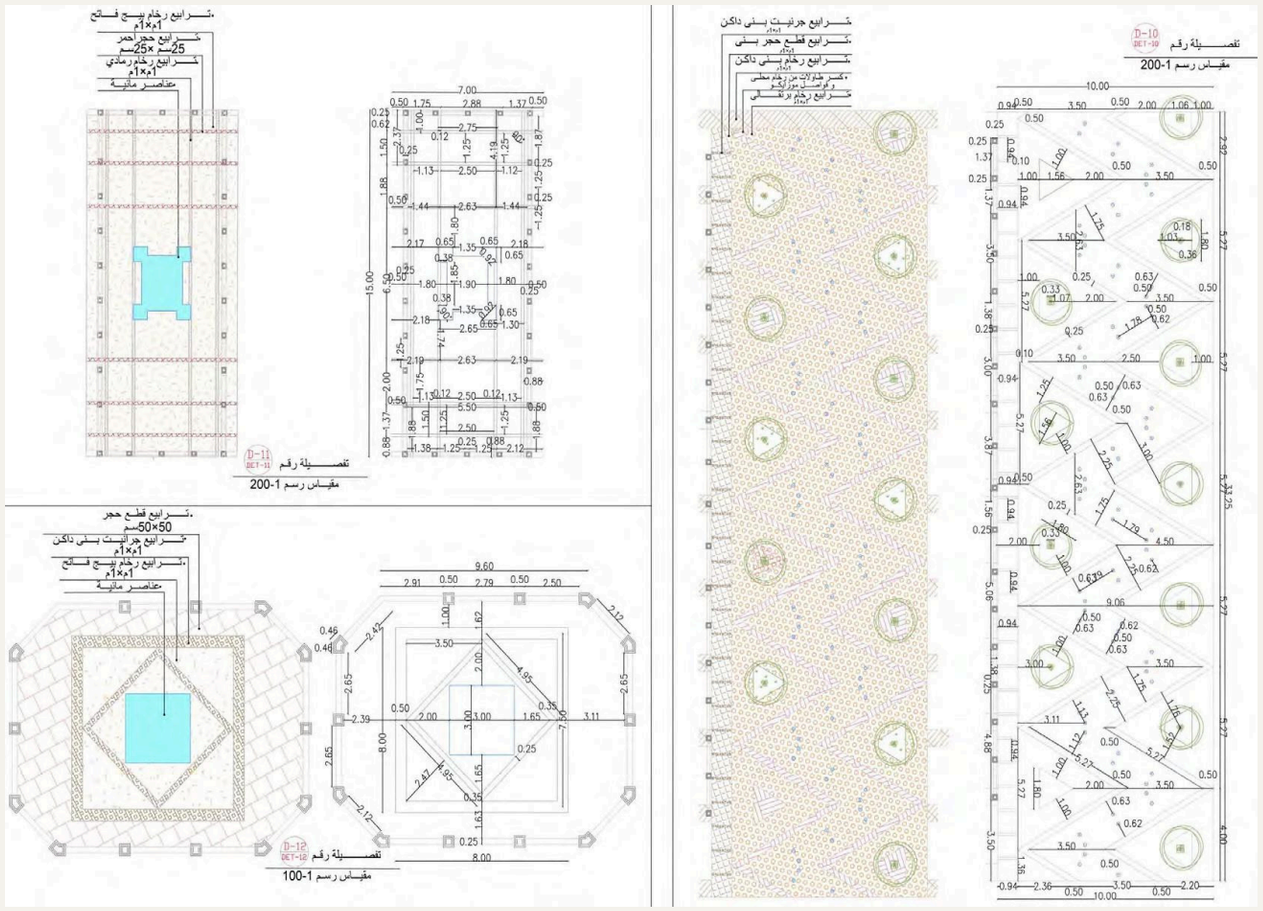

Original detail sheet: paving patterns, dimensions and feature layouts. My work focused on developing and preparing the technical drawings.

STAKING PLAN

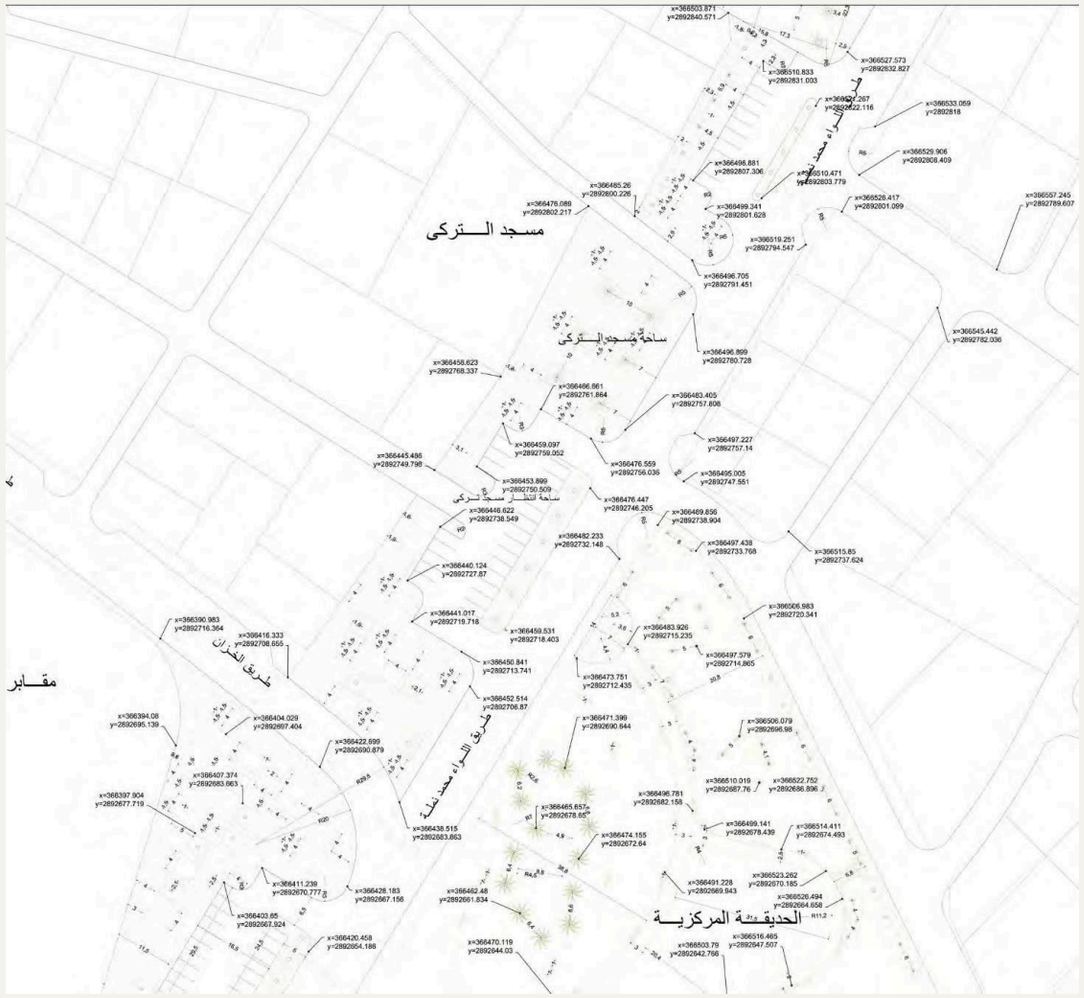

Selected staking sheet with coordinate references and element locations. Presented as construction documentation.

DRAWING EXCERPTS / NOT TO SCALE

AL BUKAYRIYAH | PUBLIC REALM IN PERSPECTIVE

Original 3D views / participation in visualization within the project team

PUBLIC-SPACE NODE

A closer view of the civic space and its relationship to the adjacent streets. The perspective complements the hardscape layouts and technical drawings.

ROLE / Participation in 3D visualization within the project team.

Context views show the surrounding street network and civic setting.

ZAKHER CITY CENTER | LAYOUTS

Visual presentation of public-space plans

01 / STREET & PEDESTRIAN INTERFACE

A LINKED PUBLIC-SPACE COMPOSITION

Plazas, patterned paving, pedestrian routes and landscape edges.

02 / PEDESTRIAN PLAZA STUDY

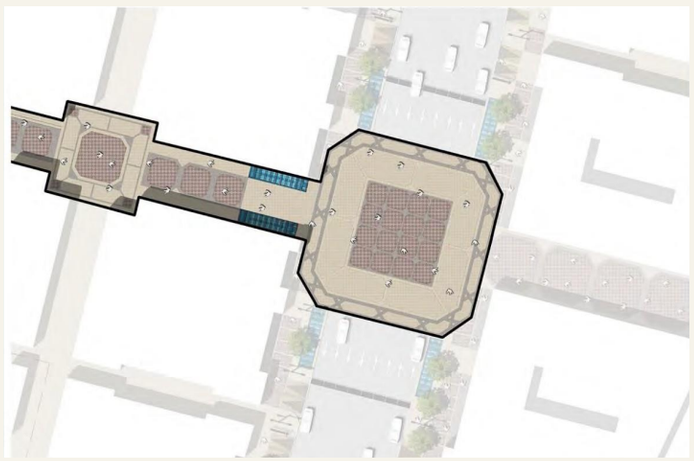

03 / CENTRAL PLAZA & CROSSING

MY CONTRIBUTION / VISUAL PRESENTATION

Prepared the visual presentation of the project plans and landscape sections.

ZAKHER CITY CENTER | SECTIONS

Visual presentation of landscape sections

04 / SHADE STRUCTURES & PUBLIC-SPACE EDGE

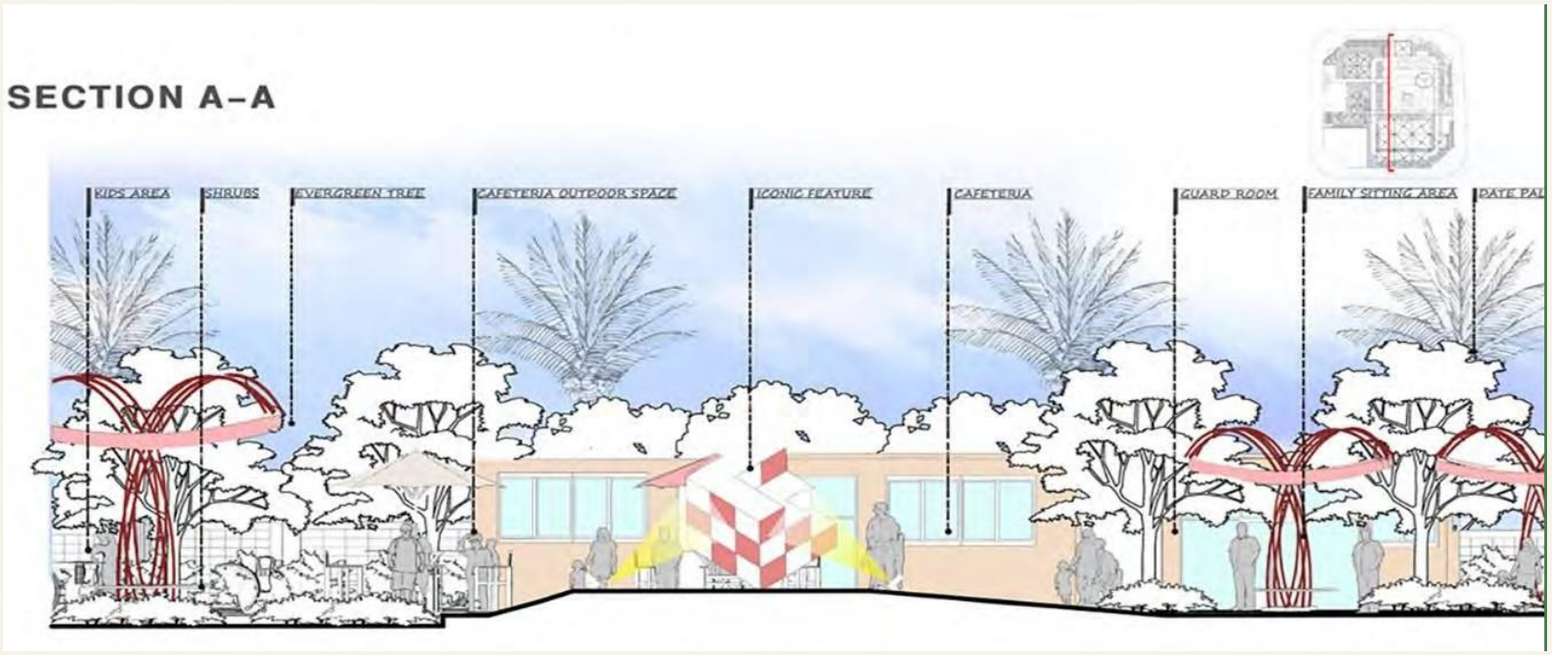

05 / COMPANION SECTION

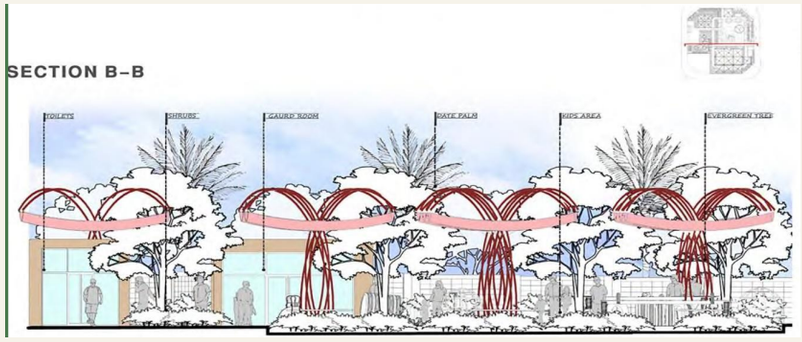

Sections communicate the spatial relationship between planting, structures and pedestrian-level spaces.

06 / PLANTING & WATER FEATURE

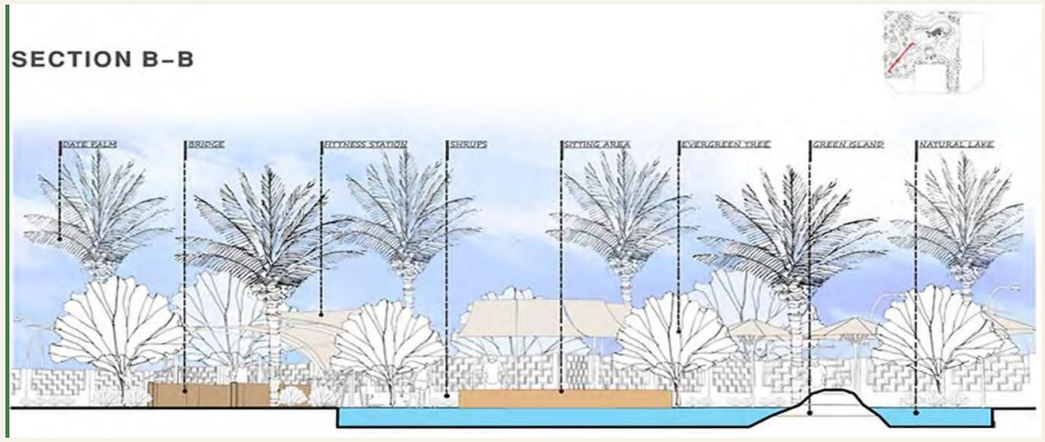

07 / LANDSCAPE & BUILT EDGE

MY CONTRIBUTION / VISUAL PRESENTATION

Prepared the visual presentation of the project plans and landscape sections.

BENI MAZAR | STRATEGIC CITY PLAN

Strategic proposal, movement analysis and functional relationships

01 / PROPOSED STRATEGIC PLAN

صوره توضح المنطقة اللوجيستية المقترحة

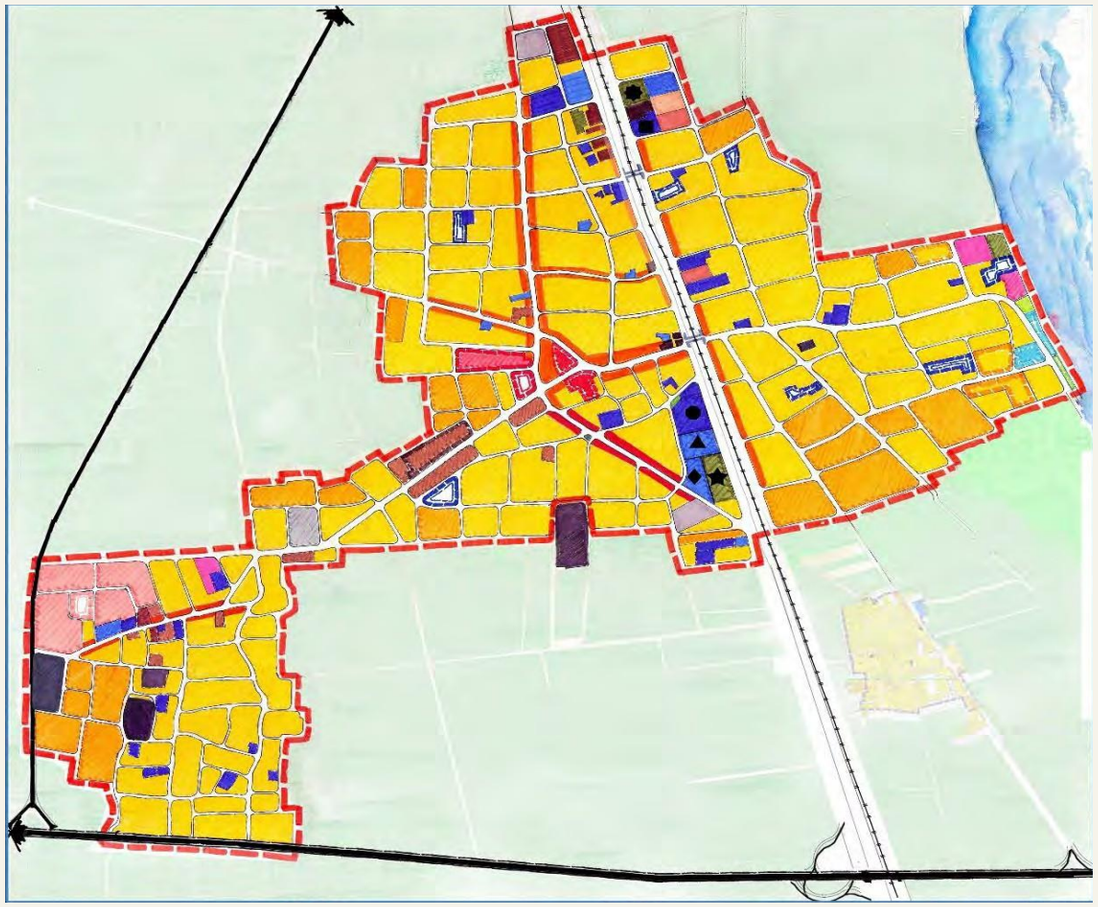

02 / MOVEMENT & ROAD ANALYSIS

03 / PROPOSED CITY VISION

04 / REGIONAL-LEVEL DEVELOPMENTS

05 / PRIMARY PLANNING DECISIONS

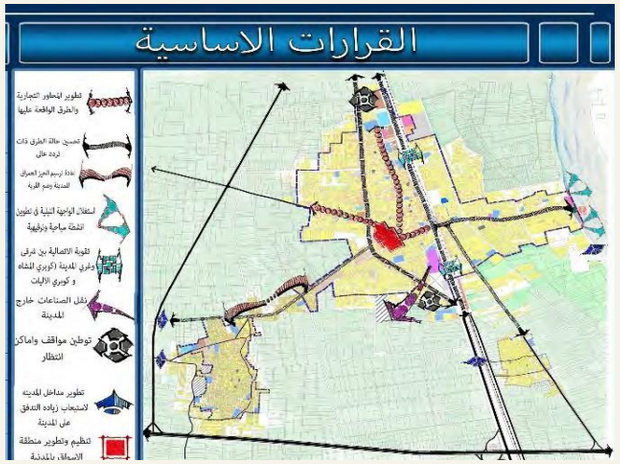

06 / FUNCTIONAL RELATIONSHIPS

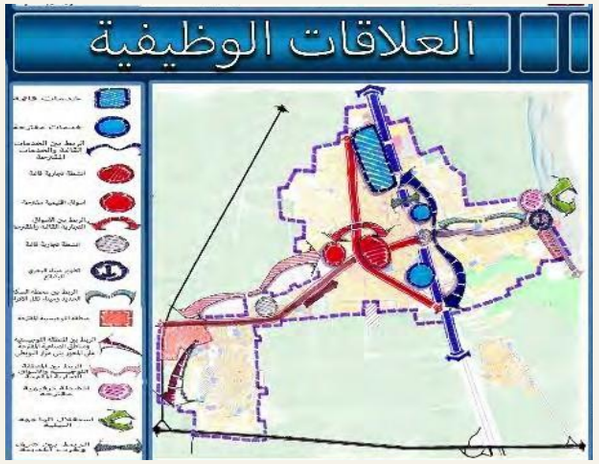

CRAFT & INDUSTRIAL DISTRICT

Workshop organization, supporting uses and spatial relationships

01 / DETAILED DISTRICT LAYOUT

02 / ACTIVITY DISTRIBUTION & CONNECTIONS

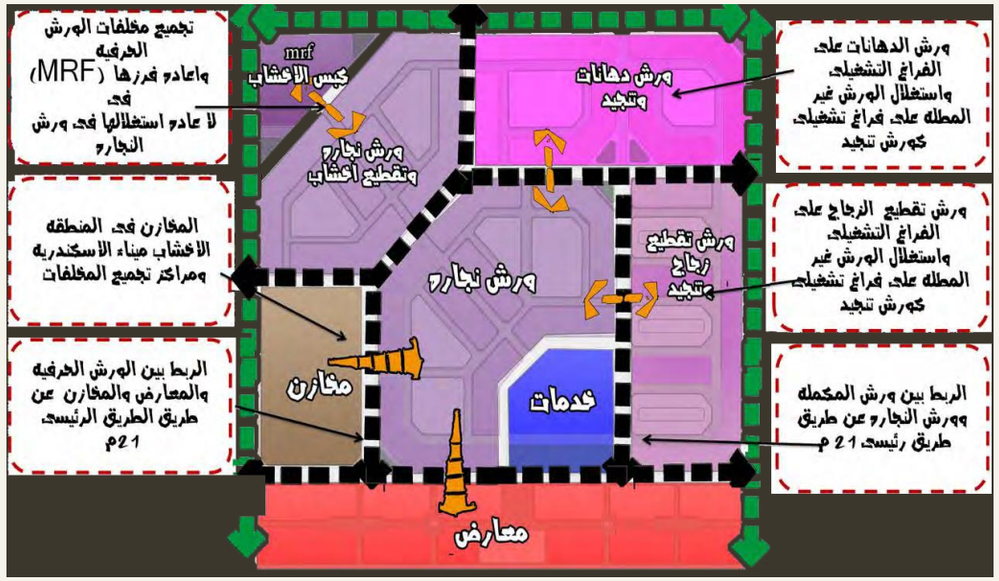

03 / ACTIVITY RELATIONSHIPS

04 / ORIGINAL 3D VIEWS

ACADEMIC DESIGN PROPOSAL

Workshop uses, services and exhibition areas.

CONTACT

AHMED ASHRAF ABDELMAKSOUD

FINAA / AI-generated visualization of the proposed design

PLANNING / DESIGN / SPATIAL ANALYSIS

Selected professional work and academic studies. Individual contributions are described within the project pages.

URBAN PLANNER & URBAN DESIGNER

Madinah, Saudi Arabia

EMAIL

ahmedashraf66@gmail.com

SAUDI ARABIA

+966 55 482 2656

EGYPT

+20 101 592 1008

LINKEDIN

ahmed-ashraf-067174107

PORTFOLIO / OCTOBER 2026
Prepared for professional review.
Project drawings retain their original geometry and source detail.